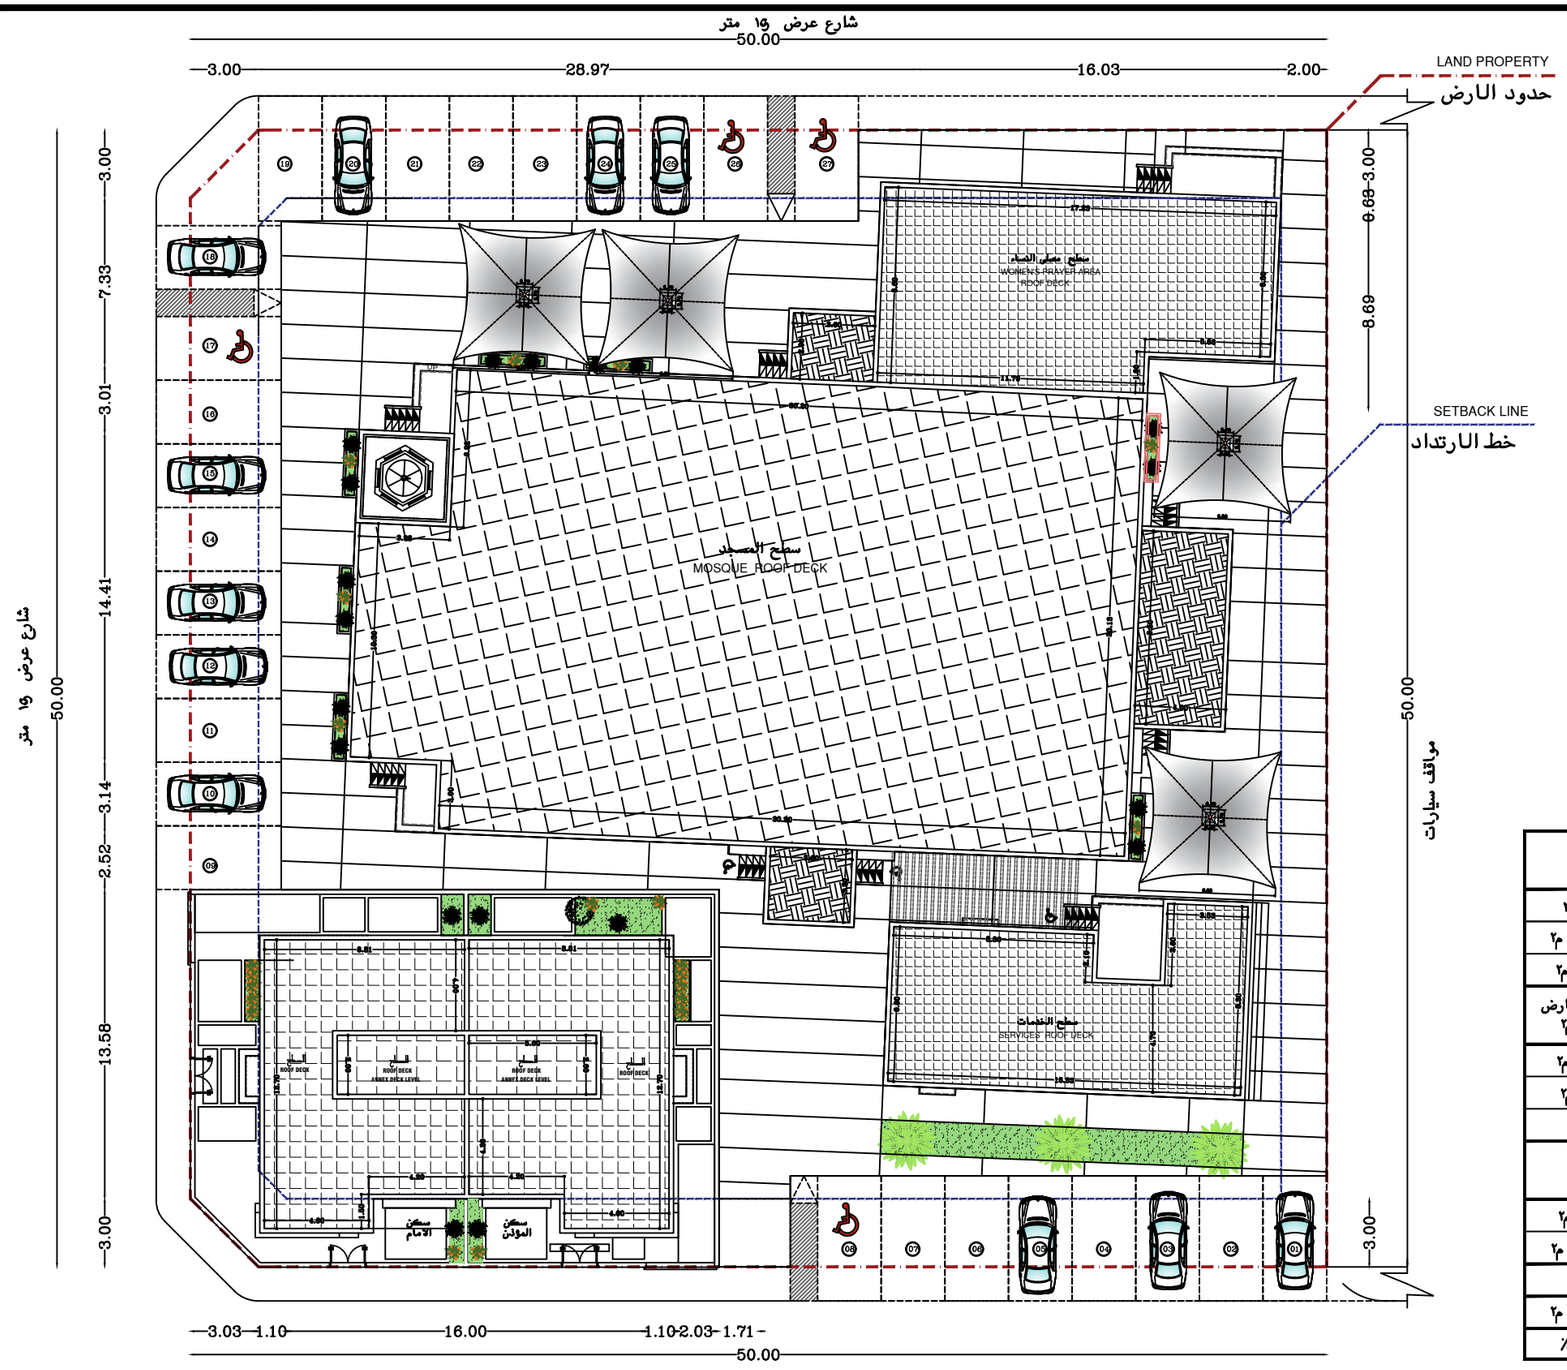


نوع التكيف المستخدم للجامع : مركزي (باكيج)

الطاقه الاستيعابيه للجامع: 700 مصلي

الطاقة الاستيعابية للمظلات الخارجية: 120 مصلي

المسجد	٢م٨٩٥,٨٩
مصلى الرجال	٦٠٠ م٢
مصلى النسا	١٠١,٠٠ م٢
مداخل وخدمات	١٦٣,٠٠ م٢
سكن الامام والمؤذن	مساحة الارض ٣٨١,٩ م٢
مساحة الدور الارضى	١٩٥,٠٠ م٢
مساحة الدور الاول	٢٢٦,١ م٢
مساحة الملحق العلوى	
الخدمات (دورات المياه + محلات)	
مساحة دورات المياه رجال	١١٢,٨٠ م٢
مساحة دورات المياه نسا	٣١,٠٠ م٢
اجمالى مساحة البنا للدور الارضى	١٣٩٢,٥٢ م٢
نسبة البنا للدور الارضى	٥٦٪

شارع عرض ١٥ متر

شركة ايدي كون للاستشارات الهندسية
C.R. 7017328449 - License: 5100000503
مطابق لكود البناء السعودي
ADCON Engineering Consultants

ADCON ENGINEERING CONSULTANTS
اديكون للاستشارات الهندسية
LICENSE : 5100000503 C.R. : 2051230629
TEL : 054 - 4591667 P . O . BOX : 32272 / 3912

PRAYER'S DIRECTION

General Notes:

1. ALL DIMENSIONS ARE IN MM AND ANGLES IN DEGREES UNLESS OTHERWISE NOTED.
2. INTERIOR DESIGN DRAWINGS MUST ALWAYS BE READ IN CONJUNCTION WITH ALL OTHER RELEVANT SERVICES DRAWINGS AND CONTRACT DOCUMENTS.
3. ALL EXISTING OR PROPOSED ELEVATIONS (LEVELS) AND DIMENSIONS, ON SITE AND ON DRAWINGS MUST BE CHECKED AND VERIFIED BY THE CONTRACTOR BEFORE THE PREPARATION OF SHOP DRAWINGS OR COMMENCEMENT OF ANY ITEM OF WORK ON THE SITE.
4. ANY DISCREPANCY BETWEEN THESE DRAWINGS AND DOCUMENTS SHOULD BE REPORTED TO THE ENGINEER FOR CLARIFICATION AND VERIFICATION.

Keyplan:

م . معمارى ARCHITECT	م/ يوسف حراز
م . كهربائى ELEC. ENGR.	
م . ميكانيكا MECH. ENGR.	
رسام اول DRAFTS MAN	م/ محمد سالى
تدقيق المهندس ENGINEER CHECKER	م/ امل البقمى

المشـــــروع	مسجد
المـــــالك	وزارة الشؤون الاسلامية والثقافية
المـــــوقع	الدمام
رقم المخطط TOWN PLAN No.	١/٧٥
رقم القطعة LOT No.	خ/ب
التـــاريخ DATE	

جدول المساحات

مساحة القبـــو BASEMENT FLOOR AREA	٠,٠٠ م٢ 00.00 sq.m	مساحة الارض LOT AREA	٢٤٩١,٠٠ م٢ 2491.00 sq.m
مساحة الدور الارضى GROUND FLOOR AREA	١٩٥,٠٠ م٢ 195.00 sq.m	مصلى الرجال	٦٠٠ م٢ 600.00 sq.m
مساحة الدور الاول FIRST FLOOR AREA	٢٢٦,١٠ م٢ 226.10 sq.m	مصلى النسا	١٠١,٠٠ م٢ 101.00 sq.m
مساحة الملحق الارضى ADD'L FLOOR AREA	٠,٠٠ م٢ 00.00 sq.m	مداخل وخدمات	١٦٣,٠٠ م٢ 163.00 sq.m
مساحة الملحق العلوى EXTENSION FLR AREA	٣١٧,١٦ م٢ 317.16 sq.m	نسبة البناء LOT COVERAGE%	٥٦,٠٠ ٪ 56.00 %

	Description	Date	Rev.

Project Name:
Address :
Owner :

Plan :
Scale : 1-10 MTS

Drawing Title:
المسقط الافقى للدور الارضى

Project Code:	Drawing No. : 01	Revision:

نوع التكيف المستخدم للجامع : مركزي (باكيج)

الطاقه الاستيعابيه للجامع: 700 مصلي

الطاقة الاستيعابية للمظلات الخارجية: 120 مصلي



المسجد	٨٩٥,٨٩ م٢
مصلى الرجال	٦٠٠ م٢
مصلى النسا	١٠١,٠٠ م٢
مداخل وخدمات	١٦٣,٠٠ م٢
سكن الامام والمؤذن	مساحة الارض ٣٨١,٩ م٢
مساحة الدور الارضى	١٩٥,٠٠ م٢
مساحة الدور الاول	٢٢٦,١ م٢
مساحة الملحق العلوى	
الخدمات (دورات المياه + محلات)	
مساحة دورات المياه رجال	١١٢,٨٠ م٢
مساحة دورات المياه نسا	٣١,٠٠ م٢
اجمالى مساحة البنا للدور الارضى	١٣٩٢,٥٢ م٢
نسبة البنا للدور الارضى	٥٦٪

شركة ايدي كون للاستشارات الهندسية
C.R. 7017328449 - License: 5100000503
مطابق لكود البناء السعودي
ADCON Engineering Consultants

ADCON ENGINEERING CONSULTANTS
اديكون للاستشارات الهندسية
LICENSE : 5100000503 C.R. : 2051230629
TEL : 054 - 4591667 P . O . BOX : 32272 / 3912

PRAYER'S DIRECTION

General Notes:

1. ALL DIMENSIONS ARE IN MM AND ANGLES IN DEGREES UNLESS OTHERWISE NOTED.
2. INTERIOR DESIGN DRAWINGS MUST ALWAYS BE READ IN CONJUNCTION WITH ALL OTHER RELEVANT SERVICES DRAWINGS AND CONTRACT DOCUMENTS.
3. ALL EXISTING OR PROPOSED ELEVATIONS (LEVELS) AND DIMENSIONS, ON SITE AND ON DRAWINGS MUST BE CHECKED AND VERIFIED BY THE CONTRACTOR BEFORE THE PREPARATION OF SHOP DRAWINGS OR COMMENCEMENT OF ANY ITEM OF WORK ON THE SITE.
4. ANY DISCREPANCY BETWEEN THESE DRAWINGS AND DOCUMENTS SHOULD BE REPORTED TO THE ENGINEER FOR CLARIFICATION AND VERIFICATION.

Keyplan:

م . معمارى ARCHITECT	م/ يوسف حراز
م . كهربائى ELEC. ENGR.	
م . ميكانيكا MECH. ENGR.	
رسام اول DRAFTS MAN	م/ محمد سالى
تدقيق المهندس ENGINEER CHECKER	م/ امل البقمى

المشـــــروع	مسجد
المـــــالك	وزارة الشؤون الاسلامية والثقافية
المـــــوقع	الدمام
رقم المخطط TOWN PLAN No.	١/٧٥
رقم القطعة LOT No.	خ/ب
التـــاريخ DATE	

جدول المساحات

مساحة القبـــو BASEMENT FLOOR AREA	٠,٠٠ م٢ 00.00 sq.m	مساحة الارض LOT AREA	٢٤٩١,٠٠ م٢ 2491.00 sq.m
مساحة الدور الارضى GROUND FLOOR AREA	١٩٥,٠٠ م٢ 195.00 sq.m	مصلى الرجال	٦٠٠ م٢ 600.00 sq.m
مساحة الدور الأول FIRST FLOOR AREA	٢٢٦,١٠ م٢ 226.10 sq.m	مصلى النسا	١٠١,٠٠ م٢ 101.00 sq.m
مساحة الملحق الارضى ADD'L FLOOR AREA	٠,٠٠ م٢ 00.00 sq.m	مداخل وخدمات	١٦٣,٠٠ م٢ 163.00 sq.m
مساحة الملحق العلوى EXTENSION FLR AREA	٣١٧,١٦ م٢ 317.16 sq.m	نسبة البناء LOT COVERAGE%	٥٦,٠٠ ٪ 56.00 %


Description	Date	Rev.

Project Name:
Address :
Owner :

Plan :
Scale : 1-10 MTS

Drawing Title:
المسقط الافقى للدور الارضى

Project Code:	Drawing No. :	Revision:
	01	

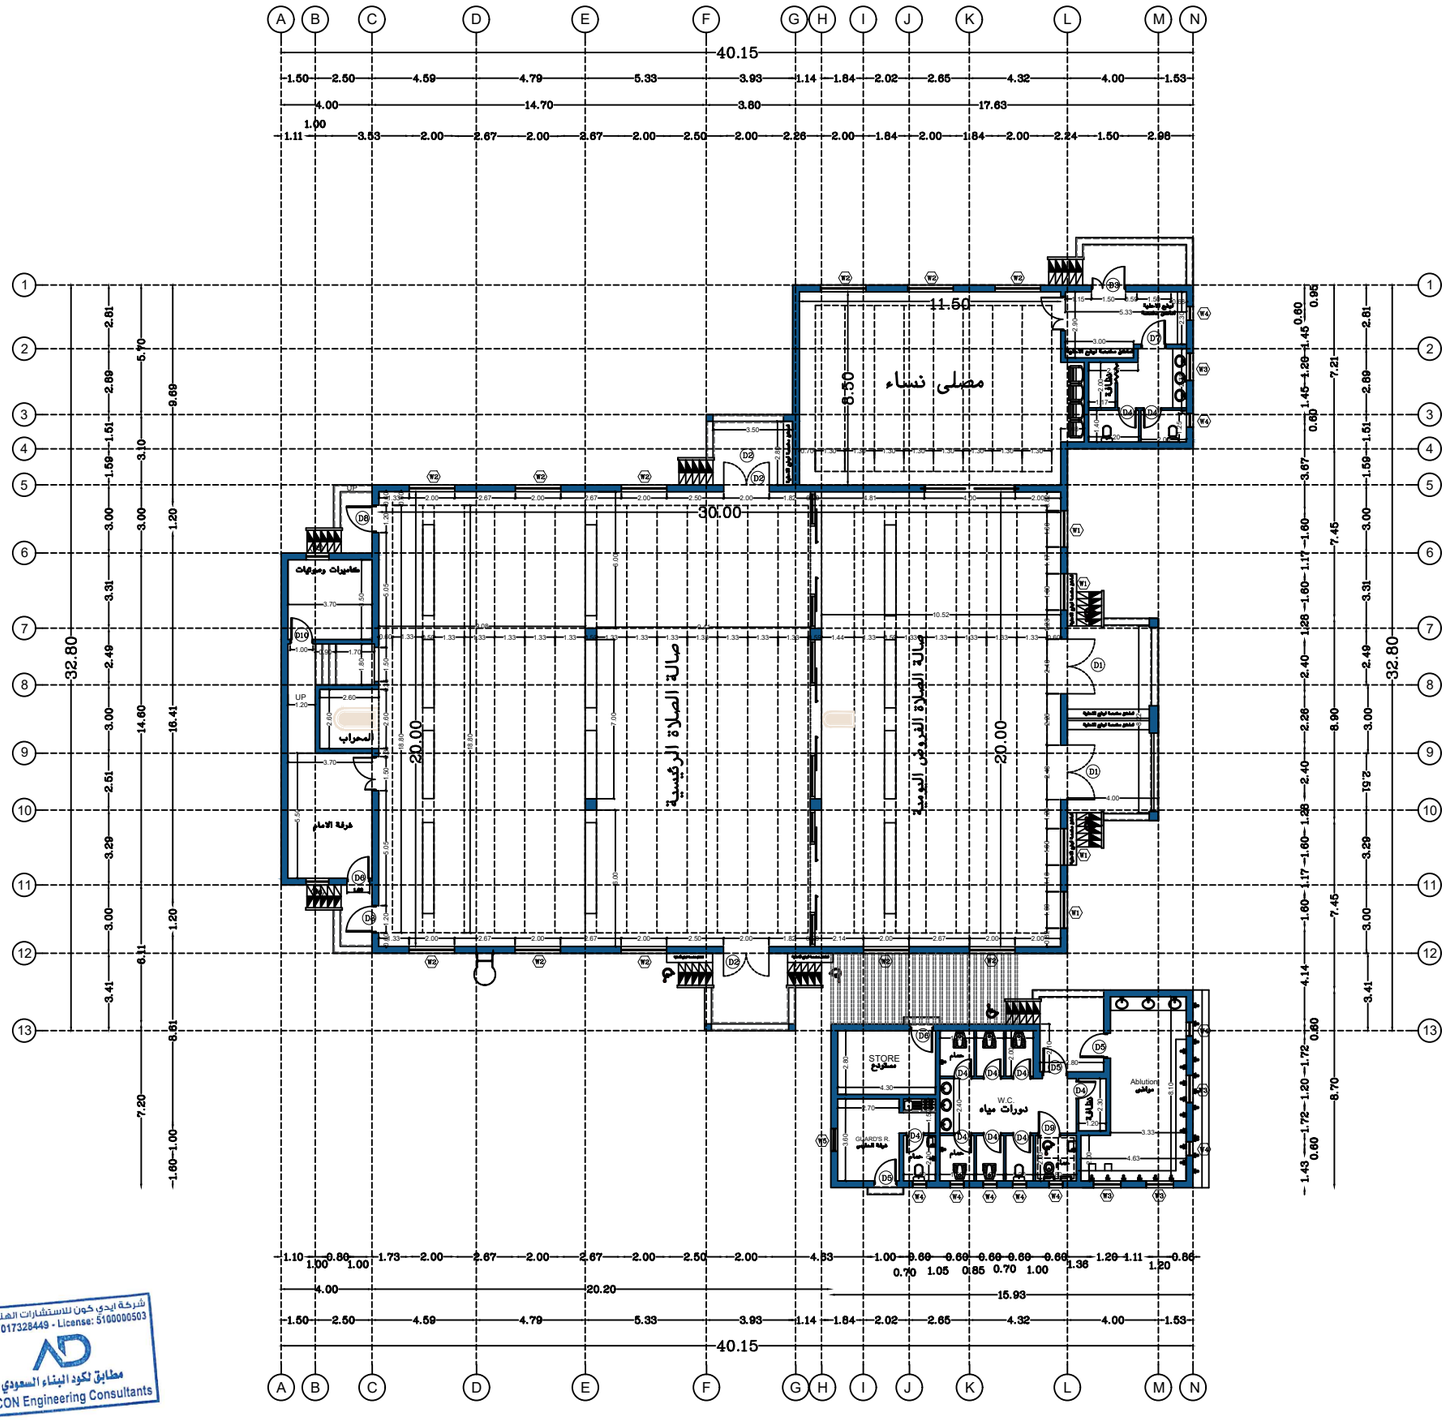

ADCON ENGINEERING CONSULTANTS
اديكون للاستشارات الهندسية
LICENSE : 5100000503 C.R. : 2051230629
TEL : 054 - 4591667 P . O . BOX : 32272 / 3912

N

General Notes:

1. ALL DIMENSIONS ARE IN MM AND ANGLES IN DEGREES UNLESS OTHERWISE NOTED.
2. INTERIOR DESIGN DRAWINGS MUST ALWAYS BE READ IN CONJUNCTION WITH ALL OTHER RELEVANT SERVICES DRAWINGS AND CONTRACT DOCUMENTS.
3. ALL EXISTING OR PROPOSED ELEVATIONS (LEVELS) AND DIMENSIONS, ON SITE AND ON DRAWINGS MUST BE CHECKED AND VERIFIED BY THE CONTRACTOR BEFORE THE PREPARATION OF SHOP DRAWINGS OR COMMENCEMENT OF ANY ITEM OF WORK ON THE SITE.
4. ANY DISCREPANCY BETWEEN THESE DRAWINGS AND DOCUMENTS SHOULD BE REPORTED TO THE ENGINEER FOR CLARIFICATION AND VERIFICATION.

Keyplan:

م . معماري ARCHITECT	م/ يوسف حراز
م . كهربائي ELEC. ENGR.	
م . ميكانيكا MECH. ENGR.	
رسام اول DRAFTS MAN	م/ محمد سالى
تدقيق المهندس ENGINEER CHECKER	م/ امل البقمى

المشـــــروع	مسجد
المـــــالك	وزارة الشؤون الاسلامية والثقافية
المـــــوقع	الدمام
رقم المخطط	١/٧٥ TOWN PLAN No.
رقم القطعة	خ/ب LOT No.
التـــاريخ	DATE

جدول المساحات

مساحة القبـــو BASEMENT FLOOR AREA	٠,٠٠ م٢ 00.00 sq.m	مساحة الارض LOT AREA	٢٤٩١,٠٠ م٢ 2491.00 sq.m
مساحة الدور الارضى GROUND FLOOR AREA	١٩٥,٠٠ م٢ 195.00 sq.m	مصلى الرجال	٦٠٠ م٢ 600.00 sq.m
مساحة الدور الاول FIRST FLOOR AREA	٢٢٦,١٠ م٢ 226.10 sq.m	مصلى النسا	١٠١,٠٠ م٢ 101.00 sq.m
مساحة الملحق الارضى ADD'L FLOOR AREA	٠,٠٠ م٢ 00.00 sq.m	مداخل وخدمات	١٦٣,٠٠ م٢ 163.00 sq.m
مساحة الملحق العلوى EXTENSION FLR AREA	٣١٧,١٦ م٢ 317.16 sq.m	نسبة البناء LOT COVERAGE	٥٦,٠٠ % 56.00 %

	Description	Date	Rev.


Project Name:
Address :
Owner :

Plan :
Scale : 1-10 MTS

Drawing Title:
المسقط الافقى للدور الارضى

Project Code:	Drawing No. :	Revision:
	01	

شركة ايدى كون للاستشارات الهندسية
C.R. 7017328449 - License: 5100000503
مطابق لكود البناء السعودي
ADCON Engineering Consultants

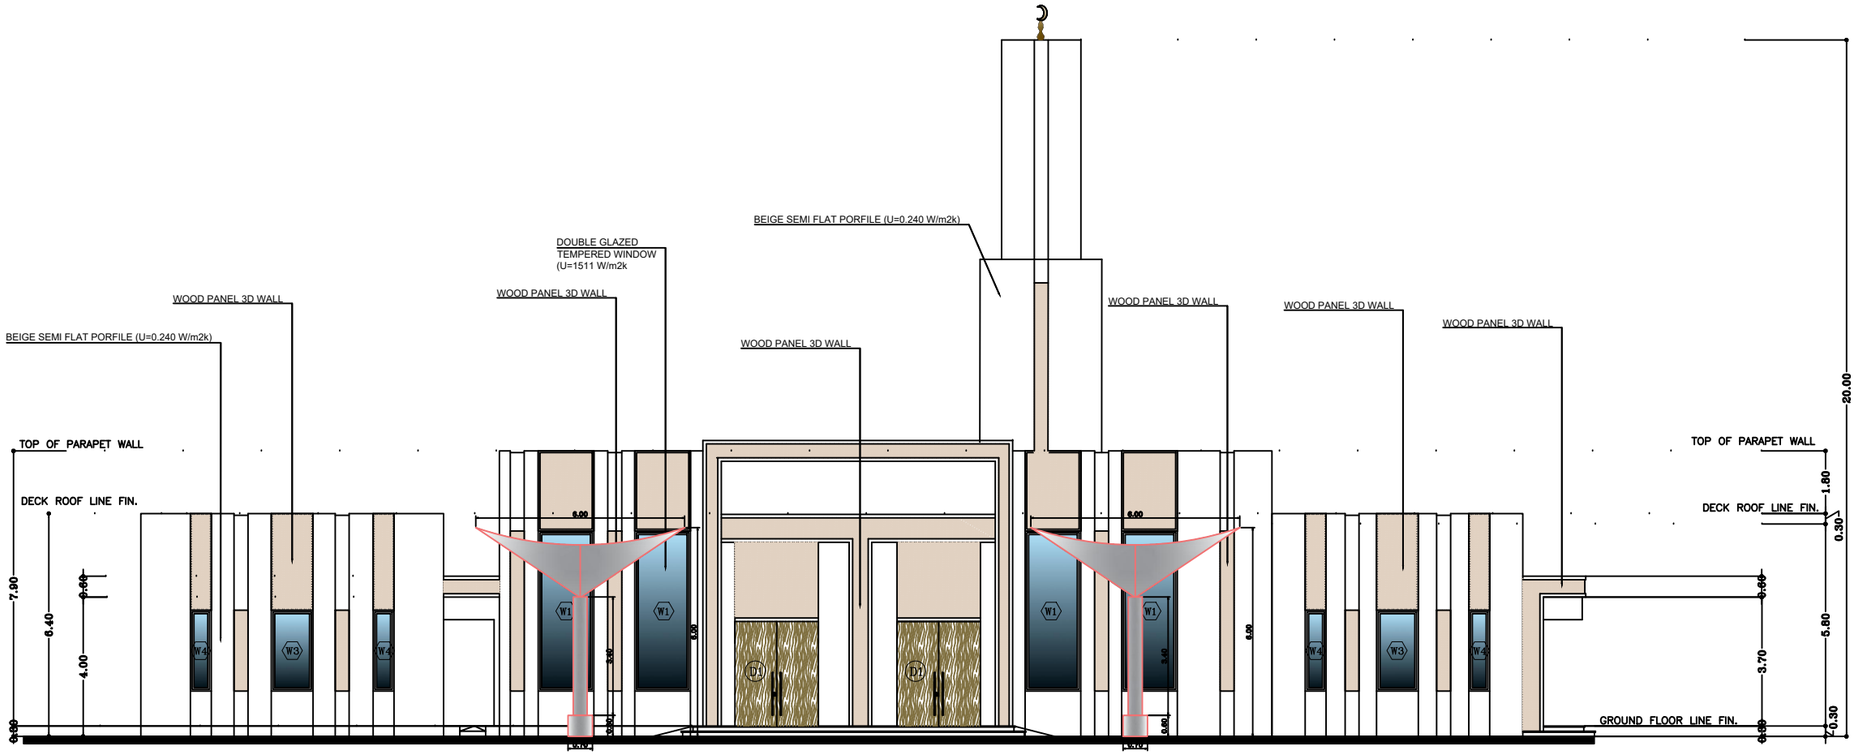

05 **MAIN ELEVATION (EAST)**
A 05 SCALE 1:100M

ADCON ENGINEERING CONSULTANTS
اديكون للاستشارات الهندسية
LICENSE : 5100000503 C.R. : 2051230629
TEL : 054 - 4591667 P . O . BOX : 32272 / 3912

General Notes:

1. ALL DIMENSIONS ARE IN MM AND ANGLES IN DEGREES UNLESS OTHERWISE NOTED.
2. INTERIOR DESIGN DRAWINGS MUST ALWAYS BE READ IN CONJUNCTION WITH ALL OTHER RELEVANT SERVICES DRAWINGS AND CONTRACT DOCUMENTS.
3. ALL EXISTING OR PROPOSED ELEVATIONS (LEVELS) AND DIMENSIONS, ON SITE AND ON DRAWINGS MUST BE CHECKED AND VERIFIED BY THE CONTRACTOR BEFORE THE PREPARATION OF SHOP DRAWINGS OR COMMENCEMENT OF ANY ITEM OF WORK ON THE SITE.
4. ANY DISCREPANCY BETWEEN THESE DRAWINGS AND DOCUMENTS SHOULD BE REPORTED TO THE ENGINEER FOR CLARIFICATION AND VERIFICATION.

Keyplan:

م/ يوسف حراز	م . معـماری ARCHITECT
	م . گهربائی ELEC. ENGR.
	م . ميكانيكا MECH. ENGR.
م/ محمد سالى	رسام اول DRAFTS MAN
م/ امل البقمى	تدقيق المهندس ENGINEER CHECKER

مسجد	المشـــــروع
وزارة الشؤون الاسلامية والثقافية	المـــــالك
الدمام	المـــــوقع
١/٧٥	رقم المخطط TOWN PLAN No.
خ/ب	رقم القطعة LOT No.
	التـــاريخ DATE

جدول المساحات

مساحة القبـــو BASEMENT FLOOR AREA	٠,٠٠ م٢ 00.00 sq.m	مساحة الارض LOT AREA	٢٤٩١,٠٠ م٢ 2491.00 sq.m
مساحة الدور الارضى GROUND FLOOR AREA	١٩٥,٠٠ م٢ 195.00 sq.m	مصلى الرجال	٦٠٠ م٢ 600.00 sq.m
مساحة الدور الاول FIRST FLOOR AREA	٢٢٦,١٠ م٢ 226.10 sq.m	مصلى النسا	١٠١,٠٠ م٢ 101.00 sq.m
مساحة الملحق الارضى ADD'L FLOOR AREA	٠,٠٠ م٢ 00.00 sq.m	مداخل وخدمات	١٦٣,٠٠ م٢ 163.00 sq.m
مساحة الملحق العلوى EXTENSION FLR AREA	٣١٧,١٦ م٢ 317.16 sq.m	نسبة البناء LOT COVERAGE %	٥٦,٠٠ ٪ 56.00 %


	Description	Date	Rev.

Project Name:
Address :
Owner :

Plan :
Scale : 1-10 MTS

Drawing Title:

Project Code:	Drawing No. :	Revision:
	01	

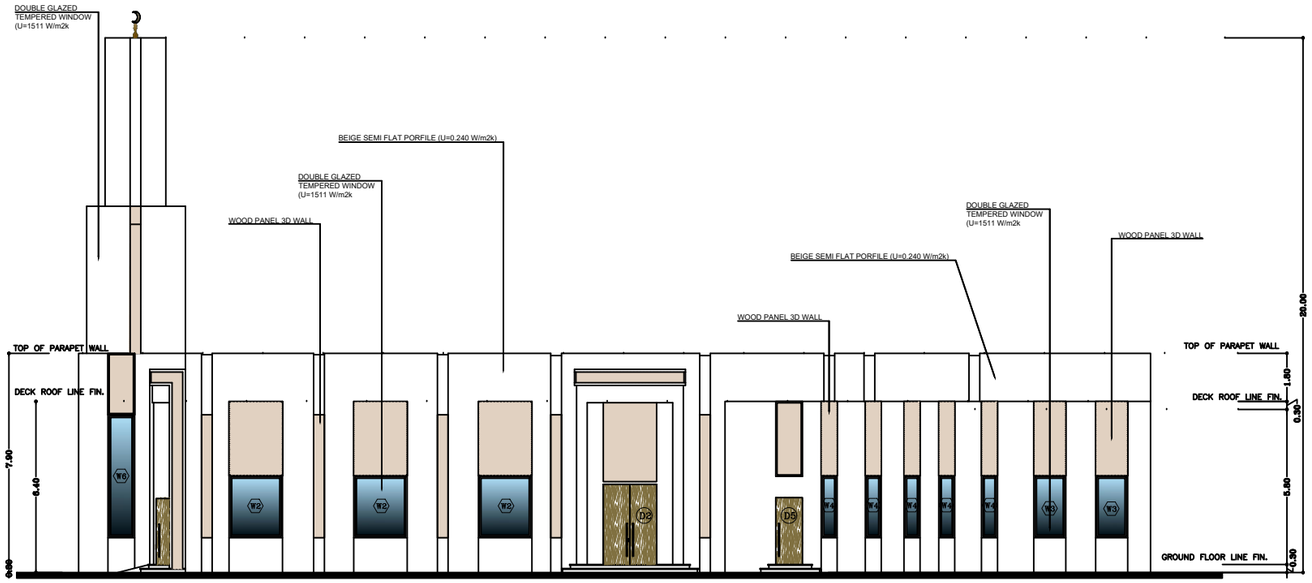

06 / A 06 **SOUTH ELEVATION**
SCALE 1:100M

شركة ايدي كون للاستشارات الهندسية
C.R. 7017328449 - License: 5100000503
مطابق لكود البناء السعودي
ADCON Engineering Consultants

General Notes:

1. ALL DIMENSIONS ARE IN MM AND ANGLES IN DEGREES UNLESS OTHERWISE NOTED.
2. INTERIOR DESIGN DRAWINGS MUST ALWAYS BE READ IN CONJUNCTION WITH ALL OTHER RELEVANT SERVICES DRAWINGS AND CONTRACT DOCUMENTS.
3. ALL EXISTING OR PROPOSED ELEVATIONS (LEVELS) AND DIMENSIONS, ON SITE AND ON DRAWINGS MUST BE CHECKED AND VERIFIED BY THE CONTRACTOR BEFORE THE PREPARATION OF SHOP DRAWINGS OR COMMENCEMENT OF ANY ITEM OF WORK ON THE SITE.
4. ANY DISCREPANCY BETWEEN THESE DRAWINGS AND DOCUMENTS SHOULD BE REPORTED TO THE ENGINEER FOR CLARIFICATION AND VERIFICATION.

Keyplan:

	Description	Date	Rev.

Project Name:

MOSQUE

Address : **DAMMAM**
Saudi Arabia

Owner :

Plan : **GROUND FLOOR PLAN**
Scale : **1:10 MTS**

ADCON ENGINEERING CONSULTANTS
اديكون للاستشارات الهندسية
LICENSE : 5100000503 C.R. : 2051230629
TEL : 054 - 4591667 P . O . BOX : 32272 / 3912


م . معماري ARCHITECT	م/ يوسف حراز	المشروع	جامع الاميرة سارة
م . كهربائي ELEC. ENGR.		المالك	وزارة الشؤن الاسلامية والاوقاف
م . ميكانيكا MECH. ENGR.		الموقع	الدمام
رسام اول DRAFTS MAN		رقم المخطط TOWN PLAN No.	١/٧٥
تدقيق المهندس ENGINEER CHECKER	م/ امل البقمى	رقم القطعة LOT No.	خ١/ب
		التاريخ DATE	

COMPUTATION OF AREAS جدول المساحات

مساحة الارض LOT AREA	٢٤٩١.٠٠ م٢ 2491.00sq.m	مساحة الملحق العلوى EXTENSION FLR AREA	م٢ sq.m
مساحة القبـــو BASEMENT FLOOR AREA	٠.٠٠ م٢ 00.00 sq.m	مساحة الميزانين MIZZANINE FLOOR	٠.٠٠ م٢ 00.00 sq.m
مساحة الدور الارضى GROUND FLOOR AREA	م٢ sq.m	طول الوارش PARAPET WALL	00.00 l.m.
مساحة الدور الاول FIRST FLOOR AREA	٠.٠٠ م٢ 00.00 sq.m	طول السور FENCE WALL	l.m.
مساحة الملحق الارضى ADD'L FLOOR AREA	٠.٠٠ م٢ 00.00 sq.m	نسبة البناء % LOT COVERAGE	%

Drawing Title:

Project Code:	Drawing No. :	Revision:
24-071	ID-GF-01	

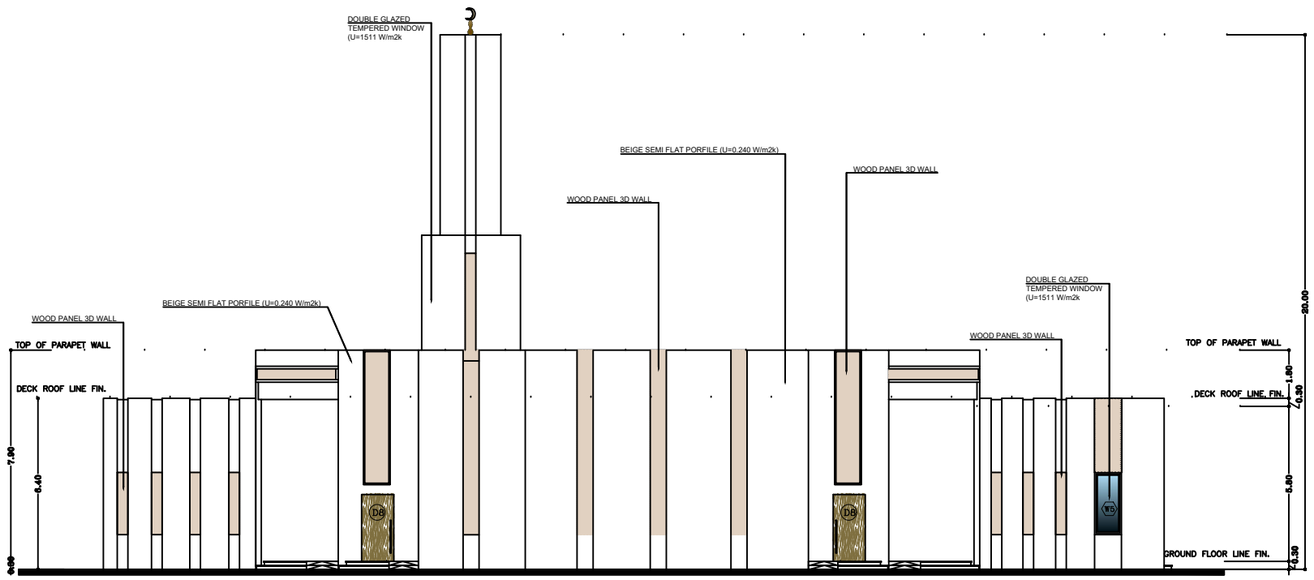

شركة ايدي كون للاستشارات الهندسية
C.R. 7017328449 - License: 5100000503
مطابق لكود البناء السعودي
ADCON Engineering Consultants

08 / A 08 **NORTH ELEVATION**
SCALE 1:100M

General Notes:

1. ALL DIMENSIONS ARE IN MM AND ANGLES IN DEGREES UNLESS OTHERWISE NOTED.
2. INTERIOR DESIGN DRAWINGS MUST ALWAYS BE READ IN CONJUNCTION WITH ALL OTHER RELEVANT SERVICES DRAWINGS AND CONTRACT DOCUMENTS.
3. ALL EXISTING OR PROPOSED ELEVATIONS (LEVELS) AND DIMENSIONS, ON SITE AND ON DRAWINGS MUST BE CHECKED AND VERIFIED BY THE CONTRACTOR BEFORE THE PREPARATION OF SHOP DRAWINGS OR COMMENCEMENT OF ANY ITEM OF WORK ON THE SITE.
4. ANY DISCREPANCY BETWEEN THESE DRAWINGS AND DOCUMENTS SHOULD BE REPORTED TO THE ENGINEER FOR CLARIFICATION AND VERIFICATION.

Keyplan:

	Description	Date	Rev.

Project Name:

MOSQUE

Address : **DAMMAM**
Saudi Arabia

Owner :

Plan : **GROUND FLOOR PLAN**

Scale : **1:10 MTS**

ADCON ENGINEERING CONSULTANTS
اديكون للاستشارات الهندسية
LICENSE : 5100000503 C.R. : 2051230629
TEL : 054 - 4591667 P . O . BOX : 32272 / 3912


م . معماري ARCHITECT	م/ يوسف حراز	المشـــــروع	جامع الاميرة سارة
م . كهربائي ELEC. ENGR.		المـــــالك	وزارة الشؤن الاسلامية والاوقاف
م . ميكانيكا MECH. ENGR.		المـــــوقع	الدمام
رسام اول DRAFTS MAN		رقم المخطط TOWN PLAN No.	١/٧٥
تدقيق المهندس ENGINEER CHECKER	م/ امل البقمى	رقم القطعة LOT No.	خ١/ب
		التـــاريخ DATE	

جدول المساحات — COMPUTATION OF AREAS

مساحة الارض LOT AREA	٢٤٩١.٠٠ م٢ 2491.00sq.m	مساحة الملحق العلوى EXTENSION FLR AREA	م٢ sq.m
مساحة القبـــو BASEMENT FLOOR AREA	٠.٠٠ م٢ 00.00 sq.m	مساحة الميزانين MIZZANINE FLOOR	٠.٠٠ م٢ 00.00 sq.m
مساحة الدور الارضى GROUND FLOOR AREA	م٢ sq.m	طول الوارش PARAPET WALL	00.00 l.m.
مساحة الدور الاول FIRST FLOOR AREA	٠.٠٠ م٢ 00.00 sq.m	طول السور FENCE WALL	l.m.
مساحة الملحق الارضى ADD'L FLOOR AREA	٠.٠٠ م٢ 00.00 sq.m	نسبة البناء LOT COVERAGE %	%

Drawing Title:

Project Code:	Drawing No. :	Revision:
24-071	ID-GF-01	

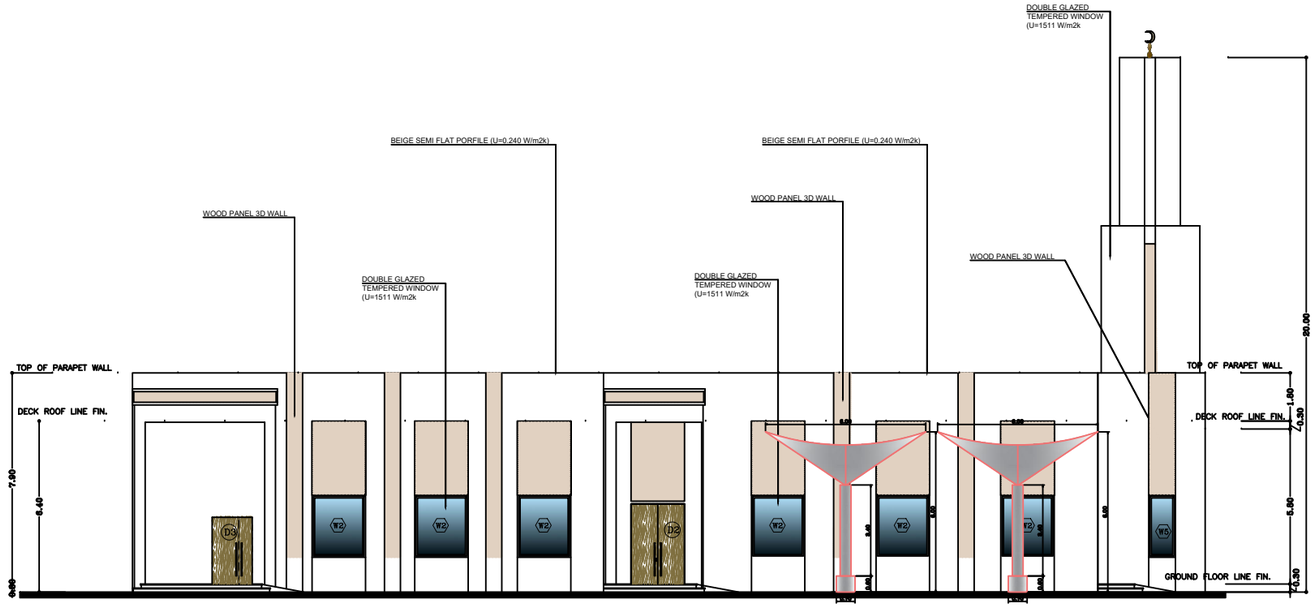

07 / A07 **WEST ELEVATION**
SCALE 1:100M

شركة ايدي كون للاستشارات الهندسية
C.R. 7017328449 - License: 5100000503
مطابق لكود البناء السعودي
ADCON Engineering Consultants

N

General Notes:

1. ALL DIMENSIONS ARE IN MM AND ANGLES IN DEGREES UNLESS OTHERWISE NOTED.
2. INTERIOR DESIGN DRAWINGS MUST ALWAYS BE READ IN CONJUNCTION WITH ALL OTHER RELEVANT SERVICES DRAWINGS AND CONTRACT DOCUMENTS.
3. ALL EXISTING OR PROPOSED ELEVATIONS (LEVELS) AND DIMENSIONS, ON SITE AND ON DRAWINGS MUST BE CHECKED AND VERIFIED BY THE CONTRACTOR BEFORE THE PREPARATION OF SHOP DRAWINGS OR COMMENCEMENT OF ANY ITEM OF WORK ON THE SITE.
4. ANY DISCREPANCY BETWEEN THESE DRAWINGS AND DOCUMENTS SHOULD BE REPORTED TO THE ENGINEER FOR CLARIFICATION AND VERIFICATION.

Keyplan:

	Description	Date	Rev.

Project Name:

MOSQUE

Address : **DAMMAM**
Saudi Arabia

Owner :

Plan : **GROUND FLOOR PLAN**

Scale : **1:10 MTS**

ADCON ENGINEERING CONSULTANTS
اديكون للاستشارات الهندسية
LICENSE : 5100000503 C.R. : 2051230629
TEL : 054 - 4591667 P . O . BOX : 32272 / 3912


م . معماري ARCHITECT	م/ يوسف حراز	المشـــروع	جامع الاميرة سارة
م . كهربائي ELEC. ENGR.		المـــالك	وزارة الشؤن الاسلامية والاوقاف
م . ميكانيكا MECH. ENGR.		المـــوقع	الدمام
رسام اول DRAFTS MAN		رقم المخطط	TOWN PLAN No. ١/٧٥
تدقيق المهندس ENGINEER CHECKER	م/ امل البقمى	رقم القطعة	LOT No. خ/ب
		التـــاريخ	DATE

COMPUTATION OF AREAS جدول المساحات

مساحة الارض LOT AREA	٢٤٩١.٠٠ م٢ 2491.00sq.m	مساحة الملحق العلوى EXTENSION FLR AREA	م٢ sq.m
مساحة القبـــو BASEMENT FLOOR AREA	٠٠.٠٠ م٢ 00.00 sq.m	مساحة الميزانين MIZZANINE FLOOR	٠٠.٠٠ م٢ 00.00 sq.m
مساحة الدور الارضى GROUND FLOOR AREA	م٢ sq.m	طول الوارش PARAPET WALL	00.00 l.m.
مساحة الدور الاول FIRST FLOOR AREA	٠٠.٠٠ م٢ 00.00 sq.m	طول السور FENCE WALL	l.m.
مساحة الملحق الارضى ADD'L FLOOR AREA	٠٠.٠٠ م٢ 00.00 sq.m	نسبة البناء LOT COVERAGE %	%

Drawing Title:

Project Code:	Drawing No. :	Revision:
24-071	ID-GF-01	

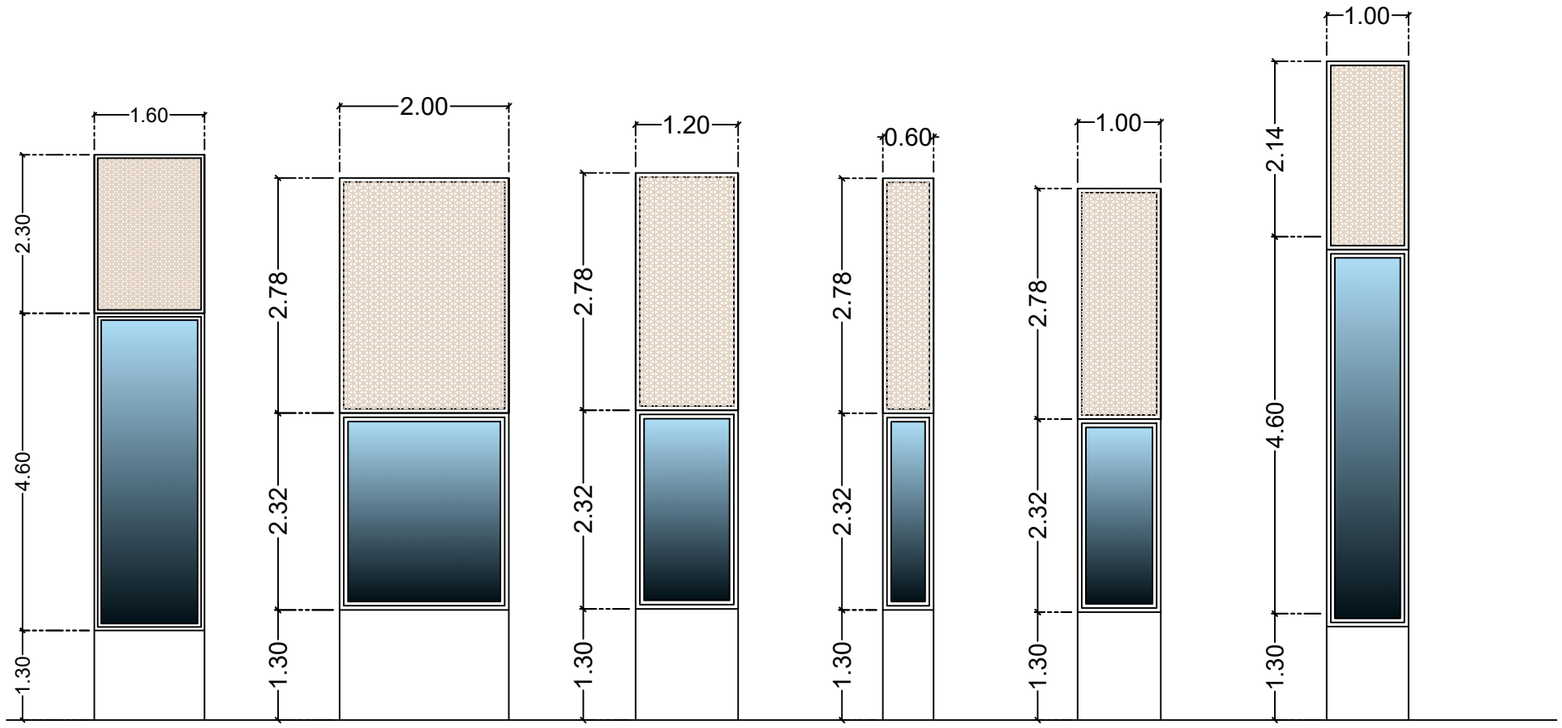

شركة ايدي كون للاستشارات الهندسية
C.R. 7017328449 - License: 5100000503
مطابق لكود البناء السعودي
ADCON Engineering Consultants

General Notes:

1. ALL DIMENSIONS ARE IN MM AND ANGLES IN DEGREES UNLESS OTHERWISE NOTED.
2. INTERIOR DESIGN DRAWINGS MUST ALWAYS BE READ IN CONJUNCTION WITH ALL OTHER RELEVANT SERVICES DRAWINGS AND CONTRACT DOCUMENTS.
3. ALL EXISTING OR PROPOSED ELEVATIONS (LEVELS) AND DIMENSIONS, ON SITE AND ON DRAWINGS MUST BE CHECKED AND VERIFIED BY THE CONTRACTOR BEFORE THE PREPARATION OF SHOP DRAWINGS OR COMMENCEMENT OF ANY ITEM OF WORK ON THE SITE.
4. ANY DISCREPANCY BETWEEN THESE DRAWINGS AND DOCUMENTS SHOULD BE REPORTED TO THE ENGINEER FOR CLARIFICATION AND VERIFICATION.

Keyplan:

	Description	Date	Rev.

Project Name:

MOSQUE

Address : **DAMMAM**
Saudi Arabia

Owner :

Plan : **GROUND FLOOR PLAN**

Scale : **1:10 MTS**

ADCON ENGINEERING CONSULTANTS
اديكون للاستشارات الهندسية
LICENSE : 5100000503 C.R. : 2051230629
TEL : 054 - 4591667 P . O . BOX : 32272 / 3912

م . معماري ARCHITECT	م/ يوسف حراز	
م . كهربائي ELEC. ENGR.		
م . ميكانيكا MECH. ENGR.		
رسام اول DRAFTS MAN		
تدقيق المهندس ENGINEER CHECKER	م/ امل البقمى	


المشـــــروع	جامع الاميرة سارة	
المـــــالك	وزارة الشؤن الاسلامية والاوقاف	
المـــــوقع	الدمام	
رقم المخطط	TOWN PLAN No.	١/٧٥
رقم القطعة	LOT No.	خ١/ب
التـــاريخ	DATE	

جدول المساحات

COMPUTATION OF AREAS					
مساحة الارض LOT AREA	٢٤٩١.٠٠ م٢ 2491.00sq.m	مساحة الملحق العلوى EXTENSION FLR AREA	م٢ sq.m		
مساحة القبـــو BASEMENT FLOOR AREA	٠.,٠٠ م٢ 00.00 sq.m	مساحة الميزانين MIZZANINE FLOOR	٠.,٠٠ م٢ 00.00 sq.m		
مساحة الدور الارضى GROUND FLOOR AREA	م٢ sq.m	طول الوارش PARAPET WALL	00.00 l.m.		
مساحة الدور الاول FIRST FLOOR AREA	٠.,٠٠ م٢ 00.00 sq.m	طول السور FENCE WALL	l.m.		
مساحة الملحق الارضى ADD'L FLOOR AREA	٠.,٠٠ م٢ 00.00 sq.m	نسبة البناء LOT COVERAGE	%		

Drawing Title:

Project Code:	Drawing No. :	Revision:
24-071	ID-GF-01	

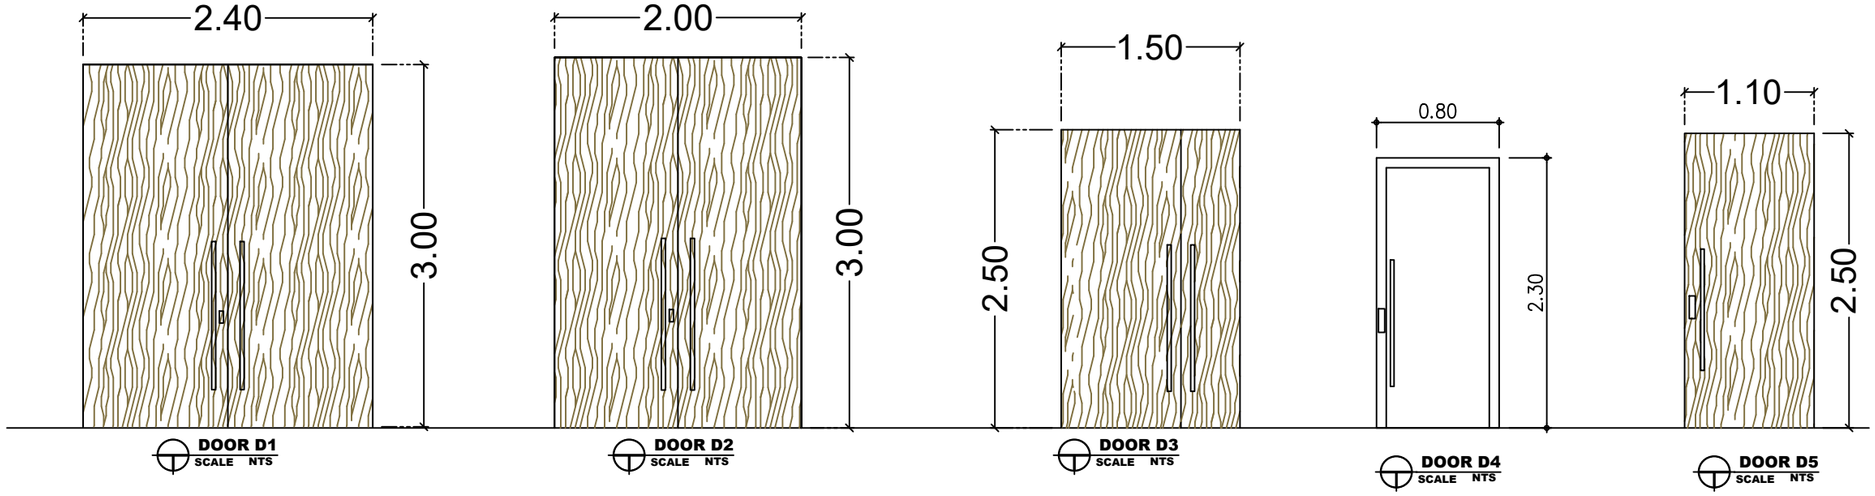


DOOR D1 SCALE NTS

DOOR D2 SCALE NTS

DOOR D3 SCALE NTS

DOOR D4 SCALE NTS

DOOR D5 SCALE NTS

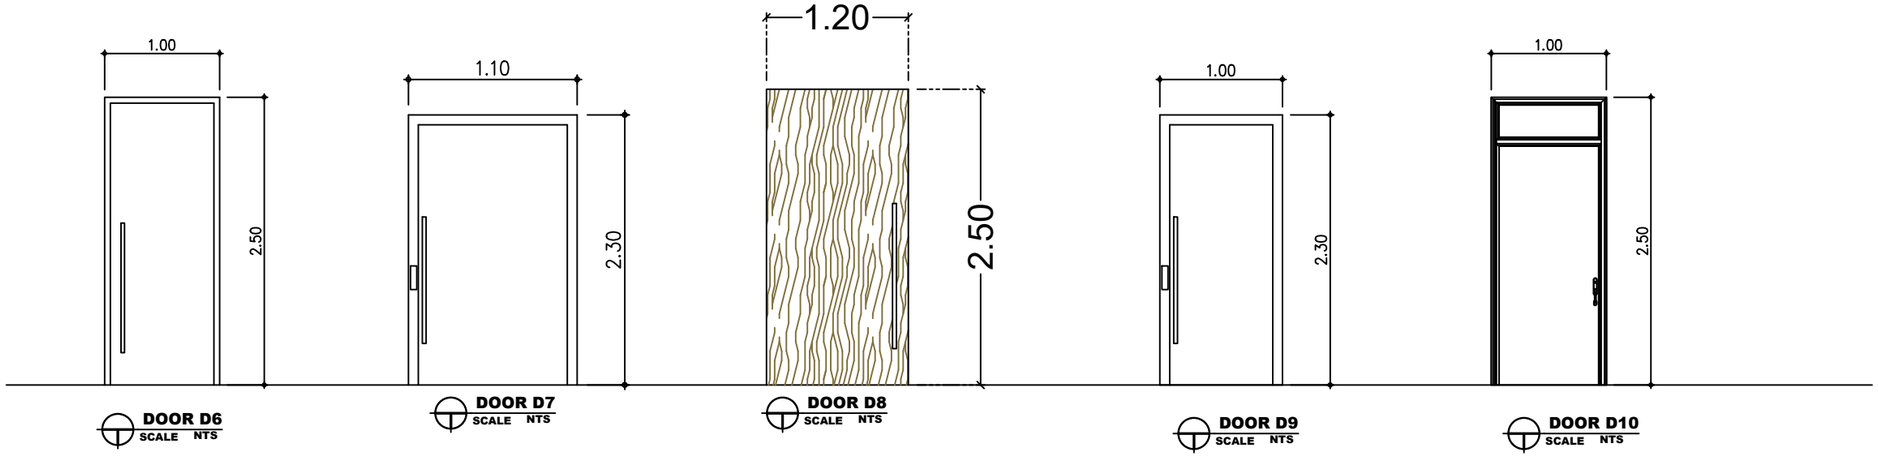

DOOR D6 SCALE NTS

DOOR D7 SCALE NTS

DOOR D8 SCALE NTS

DOOR D9 SCALE NTS

DOOR D10 SCALE NTS

General Notes:

1. ALL DIMENSIONS ARE IN MM AND ANGLES IN DEGREES UNLESS OTHERWISE NOTED.
2. INTERIOR DESIGN DRAWINGS MUST ALWAYS BE READ IN CONJUNCTION WITH ALL OTHER RELEVANT SERVICES DRAWINGS AND CONTRACT DOCUMENTS.
3. ALL EXISTING OR PROPOSED ELEVATIONS (LEVELS) AND DIMENSIONS, ON SITE AND ON DRAWINGS MUST BE CHECKED AND VERIFIED BY THE CONTRACTOR BEFORE THE PREPARATION OF SHOP DRAWINGS OR COMMENCEMENT OF ANY ITEM OF WORK ON THE SITE.
4. ANY DISCREPANCY BETWEEN THESE DRAWINGS AND DOCUMENTS SHOULD BE REPORTED TO THE ENGINEER FOR CLARIFICATION AND VERIFICATION.

Keyplan:

	Description	Date	Rev.

Project Name:

MOSQUE

Address : **DAMMAM**
Saudi Arabia

Owner :

Plan : **GROUND FLOOR PLAN**

Scale : **1:10 MTS**

ADCON ENGINEERING CONSULTANTS
اديكون للاستشارات الهندسية
LICENSE : 5100000503 C.R. : 2051230629
TEL : 054 - 4591667 P . O . BOX : 32272 / 3912

م . معماري ARCHITECT	م/ يوسف حراز	
م . كهربائي ELEC. ENGR.		
م . ميكانيكا MECH. ENGR.		
رسام اول DRAFTS MAN		
تدقيق المهندس ENGINEER CHECKER	م/ امل البقمى	


المشـــــروع	جامع الاميرة سارة	
المـــــالك	وزارة الشؤن الاسلامية والاوقاف	
المـــــوقع	الدمام	
رقم المخطط	TOWN PLAN No.	١/٧٥
رقم القطعة	LOT No.	خ١/ب
التـــاريخ	DATE	

جدول المساحات COMPUTATION OF AREAS


مساحة الارض LOT AREA	٢٤٩١.٠٠ م٢ 2491.00sq.m	مساحة الملحق العلوى EXTENSION FLR AREA	م٢ sq.m
مساحة القبـــو BASEMENT FLOOR AREA	٠٠.٠٠ م٢ 00.00 sq.m	مساحة الميزانين MIZZANINE FLOOR	٠٠.٠٠ م٢ 00.00 sq.m
مساحة الدور الارضى GROUND FLOOR AREA	م٢ sq.m	طول الوارش PARAPET WALL	00.00 l.m.
مساحة الدور الاول FIRST FLOOR AREA	٠٠.٠٠ م٢ 00.00 sq.m	طول السور FENCE WALL	l.m.
مساحة الملحق الارضى ADD'L FLOOR AREA	٠٠.٠٠ م٢ 00.00 sq.m	نسبة البناء LOT COVERAGE %	%

Drawing Title:


Project Code:	Drawing No. :	Revision:
24-071	ID-GF-01	

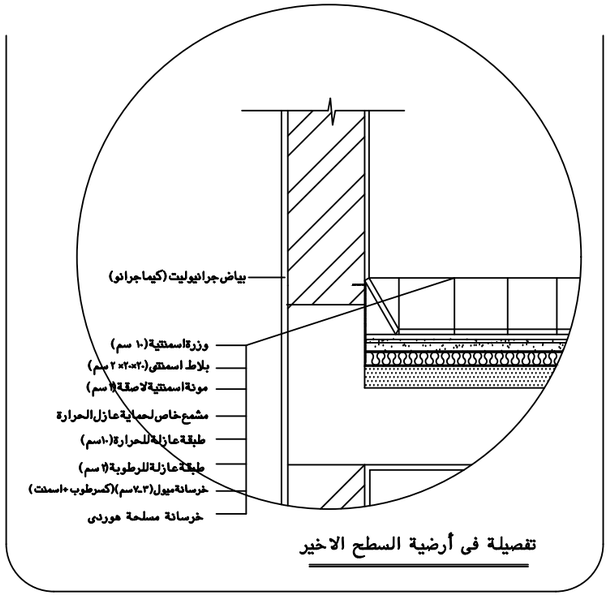

تفصيلة فى أرضية السطح الاخير

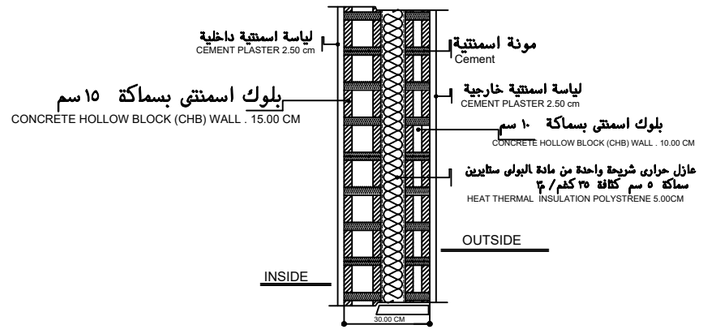

تفصيلة الجدار الخارجى المعزول حراريا
DETAIL OF THERMAL INSULATED
OUTSIDE WALL

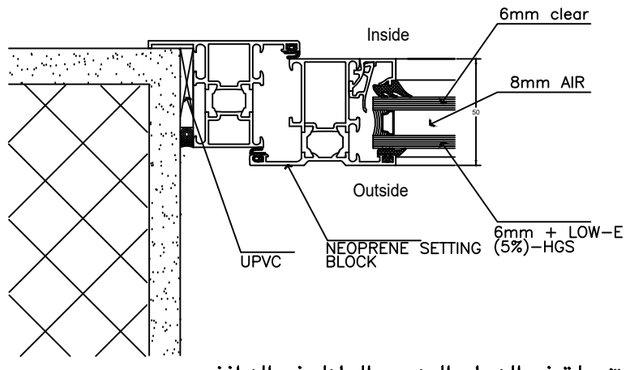

تفصيلة فى الزجاج المزدوج العازل فى النوافذ

N

General Notes:

1. ALL DIMENSIONS ARE IN MM AND ANGLES IN DEGREES UNLESS OTHERWISE NOTED.
2. INTERIOR DESIGN DRAWINGS MUST ALWAYS BE READ IN CONJUNCTION WITH ALL OTHER RELEVANT SERVICES DRAWINGS AND CONTRACT DOCUMENTS.
3. ALL EXISTING OR PROPOSED ELEVATIONS (LEVELS) AND DIMENSIONS, ON SITE AND ON DRAWINGS MUST BE CHECKED AND VERIFIED BY THE CONTRACTOR BEFORE THE PREPARATION OF SHOP DRAWINGS OR COMMENCEMENT OF ANY ITEM OF WORK ON THE SITE.
4. ANY DISCREPANCY BETWEEN THESE DRAWINGS AND DOCUMENTS SHOULD BE REPORTED TO THE ENGINEER FOR CLARIFICATION AND VERIFICATION.

Keyplan:

	Description	Date	Rev.

Project Name:

MOSQUE

Address : **DAMMAM**
Saudi Arabia

Owner :

Plan : **GROUND FLOOR PLAN**

Scale : **1:10 MTS**

ADCON ENGINEERING CONSULTANTS
اديكون للاستشارات الهندسية
LICENSE : 5100000503 C.R. : 2051230629
TEL : 054 - 4591667 P . O . BOX : 32272 / 3912


م . معمارى ARCHITECT	م/ يوسف حراز	المشـــــروع	جامع الاميرة سارة
م . كهربائى ELEC. ENGR.		المـــــــالك	وزارة الشؤن الاسلامية والاوقاف
م . ميكانيكا MECH. ENGR.		المـــــوقع	الدمام
رسام اول DRAFTS MAN		رقم المخطط TOWN PLAN No.	١/٧٥
تدقيق المهندس ENGINEER CHECKER	م/ امل البقمى	رقم القطعة LOT No.	خ١/ب
		التـــاريخ DATE	

جدول المساحات — COMPUTATION OF AREAS

مساحة الارض LOT AREA	٢٤٩١.٠٠ م٢ 2491.00sq.m	مساحة الملحق العلوى EXTENSION FLR AREA	م٢ sq.m
مساحة القبـــو BASEMENT FLOOR AREA	٠.٠٠ م٢ 00.00 sq.m	مساحة الميزانين MIZZANINE FLOOR	٠.٠٠ م٢ 00.00 sq.m
مساحة الدور الارضى GROUND FLOOR AREA	م٢ sq.m	طول الوارش PARAPET WALL	00.00 l.m.
مساحة الدور الاول FIRST FLOOR AREA	٠.٠٠ م٢ 00.00 sq.m	طول السور FENCE WALL	l.m.
مساحة الملحق الارضى ADD'L FLOOR AREA	٠.٠٠ م٢ 00.00 sq.m	نسبة البناء LOT COVERAGE %	%

Drawing Title:

Project Code:	Drawing No. :	Revision:
24-071	ID-GF-01	

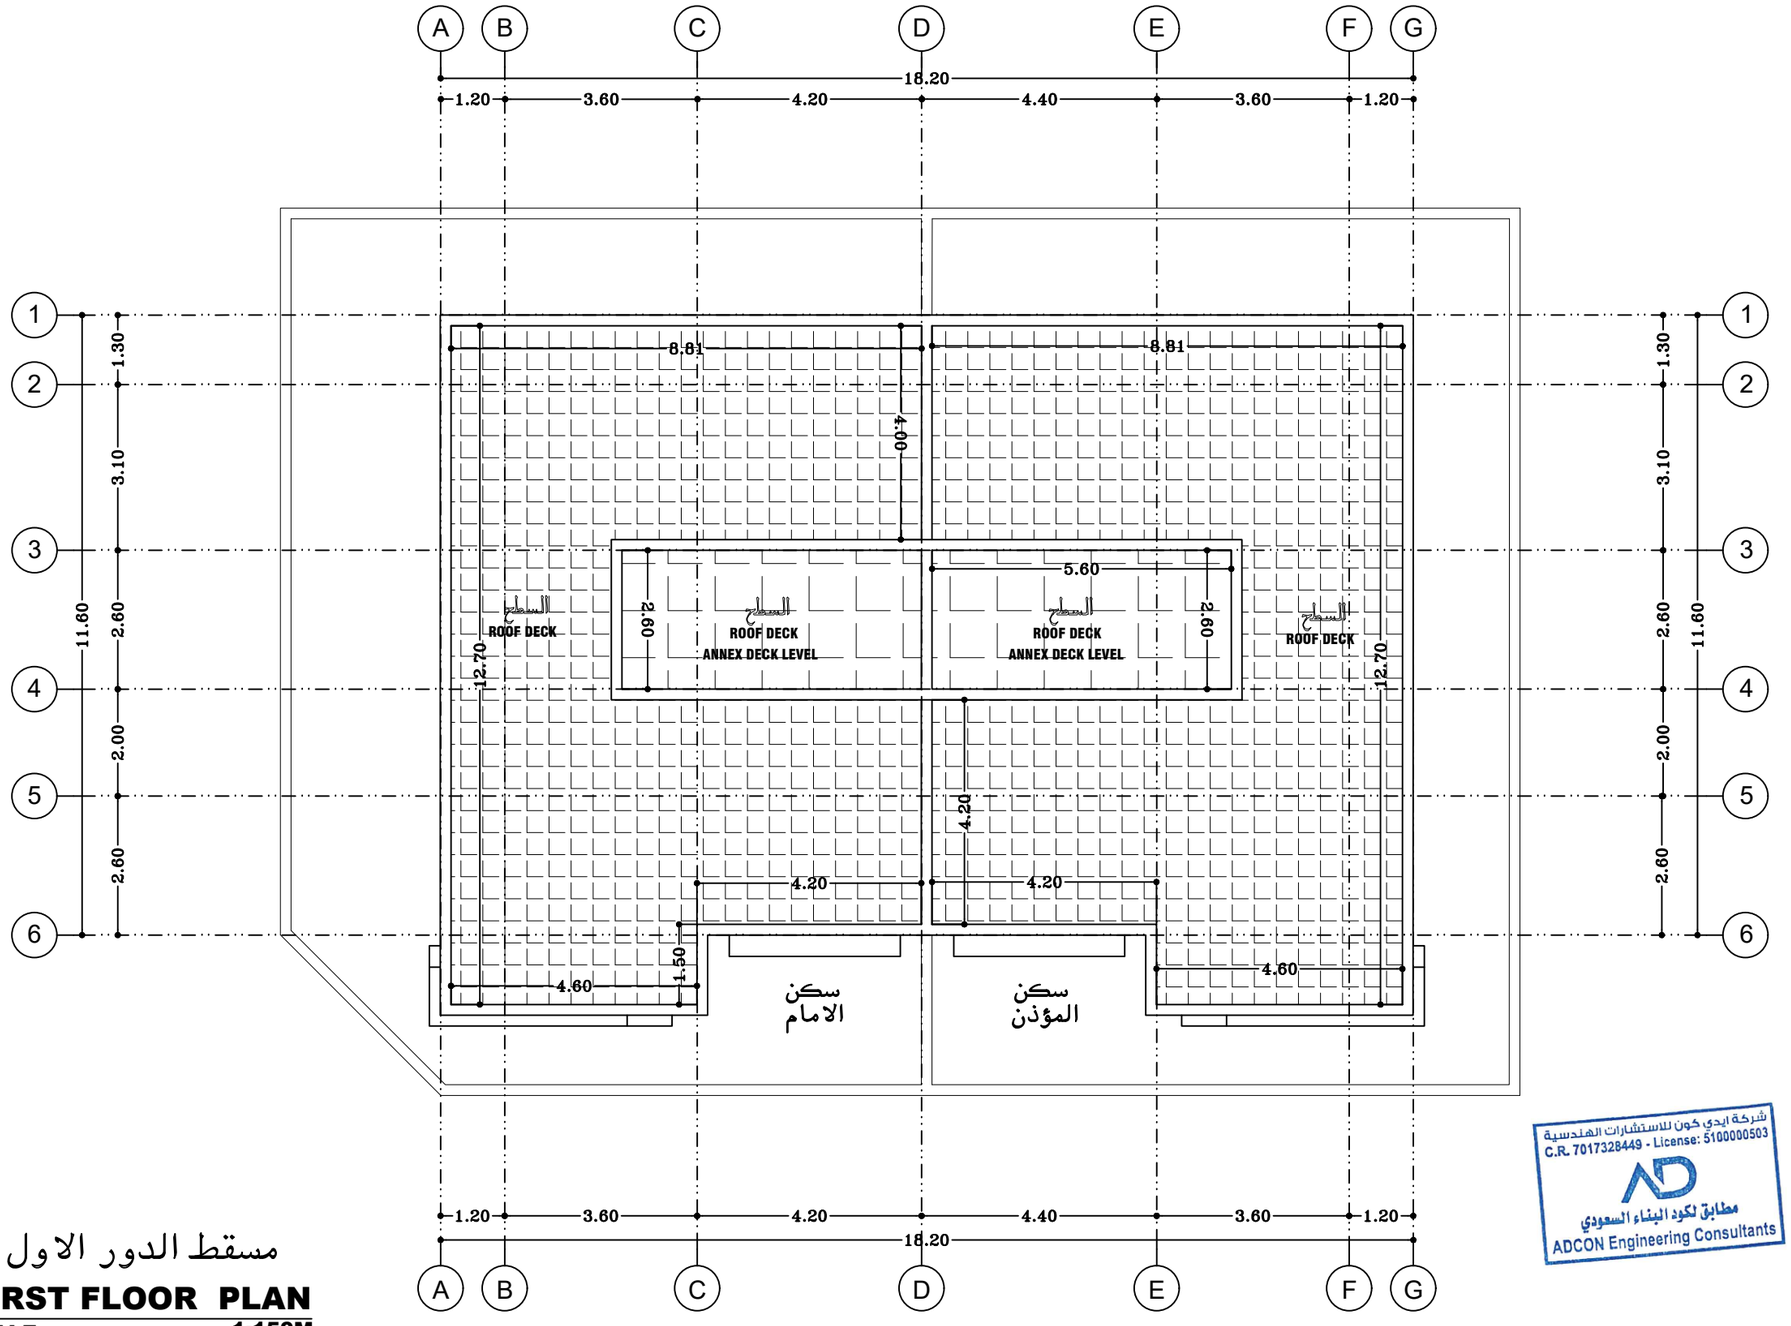

مسقط الدور الاول

FIRST FLOOR PLAN

07 / A 7

SCALE 1:150M

N

General Notes:

1. ALL DIMENSIONS ARE IN MM AND ANGLES IN DEGREES UNLESS OTHERWISE NOTED.
2. INTERIOR DESIGN DRAWINGS MUST ALWAYS BE READ IN CONJUNCTION WITH ALL OTHER RELEVANT SERVICES DRAWINGS AND CONTRACT DOCUMENTS.
3. ALL EXISTING OR PROPOSED ELEVATIONS (LEVELS) AND DIMENSIONS, ON SITE AND ON DRAWINGS MUST BE CHECKED AND VERIFIED BY THE CONTRACTOR BEFORE THE PREPARATION OF SHOP DRAWINGS OR COMMENCEMENT OF ANY ITEM OF WORK ON THE SITE.
4. ANY DISCREPANCY BETWEEN THESE DRAWINGS AND DOCUMENTS SHOULD BE REPORTED TO THE ENGINEER FOR CLARIFICATION AND VERIFICATION.

Keyplan:

	Description	Date	Rev.

شركة ايدي كون للاستشارات الهندسية
C.R. 7017328449 - License: 5100000503
مطابق لكود البناء السعودي
ADCON Engineering Consultants

Project Name:

MOSQUE

Address : **DAMMAM**
Saudi Arabia

Owner :

Plan : **GROUND FLOOR PLAN**

Scale : **1:10 MTS**

ADCON ENGINEERING CONSULTANTS
اديكون للاستشارات الهندسية
LICENSE : 5100000503 C.R. : 2051230629
TEL : 054 - 4591667 P . O . BOX : 32272 / 3912


م . معماري ARCHITECT	م/ يوسف حراز	المشروع	جامع الاميرة سارة
م . كهربائي ELEC. ENGR.		المالك	وزارة الشؤن الاسلامية والاوقاف
م . ميكانيكا MECH. ENGR.		الموقع	الدمام
رسام اول DRAFTS MAN		رقم المخطط TOWN PLAN No.	١/٧٥
تدقيق المهندس ENGINEER CHECKER	م/ امل البقمى	رقم القطعة LOT No.	خ١/ب
		التاريخ DATE	

جدول المساحات			
مساحة الارض LOT AREA	٢٤٩١.٠٠ م٢ 2491.00sq.m	مساحة الملحق العلوى EXTENSION FLR AREA	م٢ sq.m
مساحة القبو BASEMENT FLOOR AREA	٠.٠٠ م٢ 00.00 sq.m	مساحة الميزانين MIZZANINE FLOOR	٠.٠٠ م٢ 00.00 sq.m
مساحة الدور الارضى GROUND FLOOR AREA	م٢ sq.m	طول الوارش PARAPET WALL	00.00 l.m.
مساحة الدور الاول FIRST FLOOR AREA	٠.٠٠ م٢ 00.00 sq.m	طول السور FENCE WALL	l.m.
مساحة الملحق الارضى ADD'L FLOOR AREA	٠.٠٠ م٢ 00.00 sq.m	نسبة البناء % LOT COVERAGE	%

COMPUTATION OF AREAS

Drawing Title:

Project Code:	Drawing No. :	Revision:
24-071	ID-GF-01	

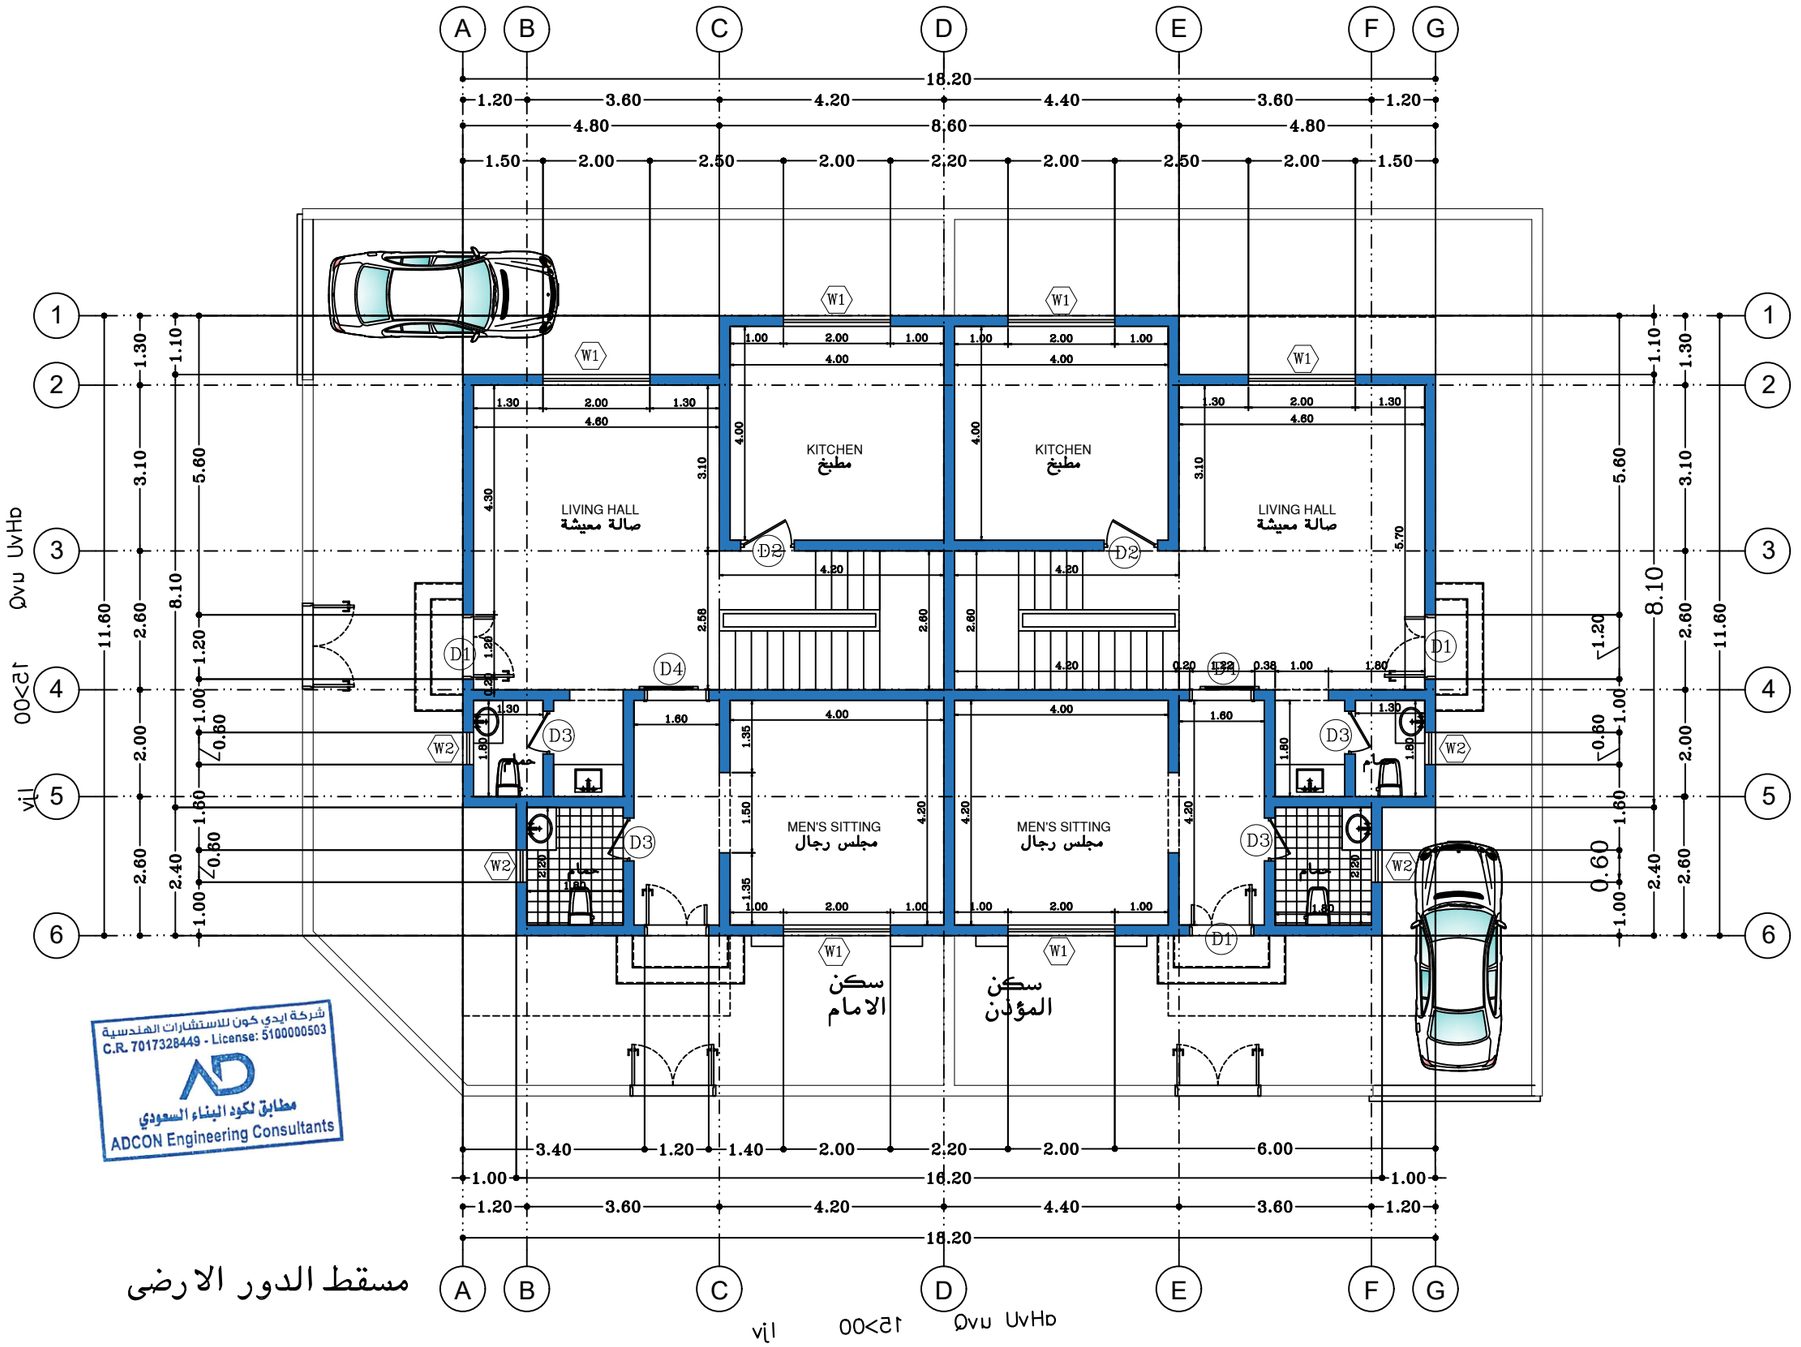

شركة ايدي كون للاستشارات الهندسية
C.R. 7017328449 - License: 5100000503
مطابق لكود البناء السعودي
ADCON Engineering Consultants

General Notes:

1. ALL DIMENSIONS ARE IN MM AND ANGLES IN DEGREES UNLESS OTHERWISE NOTED.
2. INTERIOR DESIGN DRAWINGS MUST ALWAYS BE READ IN CONJUNCTION WITH ALL OTHER RELEVANT SERVICES DRAWINGS AND CONTRACT DOCUMENTS.
3. ALL EXISTING OR PROPOSED ELEVATIONS (LEVELS) AND DIMENSIONS, ON SITE AND ON DRAWINGS MUST BE CHECKED AND VERIFIED BY THE CONTRACTOR BEFORE THE PREPARATION OF SHOP DRAWINGS OR COMMENCEMENT OF ANY ITEM OF WORK ON THE SITE.
4. ANY DISCREPANCY BETWEEN THESE DRAWINGS AND DOCUMENTS SHOULD BE REPORTED TO THE ENGINEER FOR CLARIFICATION AND VERIFICATION.

Keyplan:

	Description	Date	Rev.

Project Name:

MOSQUE

Address : **DAMMAM**
Saudi Arabia

Owner :

Plan : **GROUND FLOOR PLAN**

Scale : **1:10 MTS**

ADCON ENGINEERING CONSULTANTS
اديكون للاستشارات الهندسية
LICENSE : 5100000503 C.R. : 2051230629
TEL : 054 - 4591667 P . O . BOX : 32272 / 3912


ARCHITECT م . معمارى	م/ يوسف حراز	المشـــروع	جامع الاميرة سارة
ELEC. ENGR. م . كهربائى		المـــالك	وزارة الشؤن الاسلامية والاوقاف
MECH. ENGR. م . ميكانيكا		المـــوقع	الدمام
DRAFTS MAN رسام اول		رقم المخطط TOWN PLAN No.	١/٧٥
ENGINEER CHECKER تدقيق المهندس	م/ امل البقمى	رقم القطعة LOT No.	خ١/ب
		التـــاريخ DATE	

COMPUTATION OF AREAS جدول المساحات

مساحة الارض LOT AREA	٢٤٩١.٠٠ م٢ 2491.00sq.m	مساحة الملحق العلوى EXTENSION FLR AREA	م٢ sq.m
مساحة القبـــو BASEMENT FLOOR AREA	٠.٠٠ م٢ 00.00 sq.m	مساحة الميزانين MIZZANINE FLOOR	٠.٠٠ م٢ 00.00 sq.m
مساحة الدور الارضى GROUND FLOOR AREA	م٢ sq.m	طول الوارش PARAPET WALL	00.00 l.m.
مساحة الدور الاول FIRST FLOOR AREA	٠.٠٠ م٢ 00.00 sq.m	طول السور FENCE WALL	l.m.
مساحة الملحق الارضى ADD'L FLOOR AREA	٠.٠٠ م٢ 00.00 sq.m	نسبة البناء LOT COVERAGE %	%

Drawing Title:

Project Code:	Drawing No. :	Revision:
24-071	ID-GF-01	

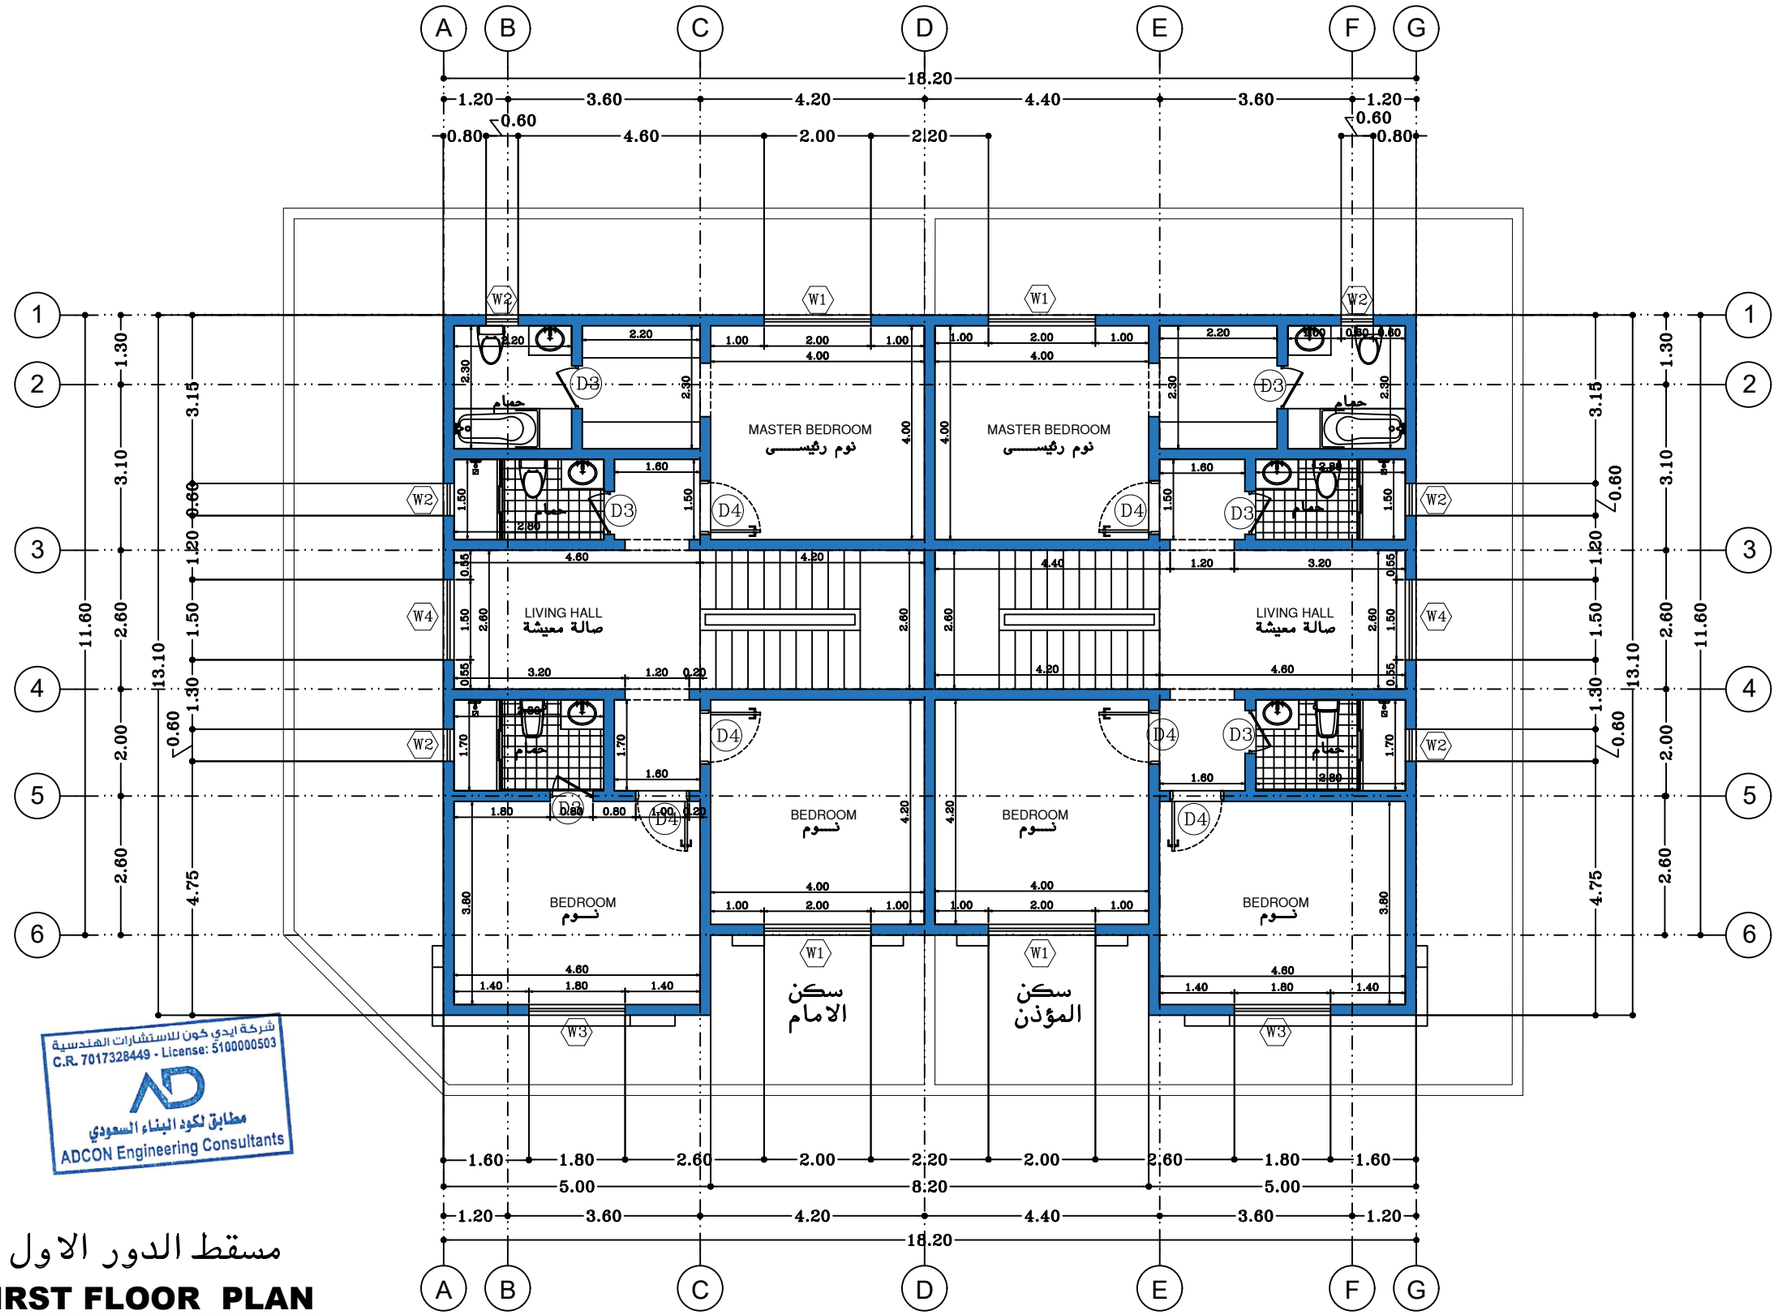

مسقط الدور الاول

FIRST FLOOR PLAN

07 / A 7

SCALE 1:150M

شركة ايدي كون للاستشارات الهندسية
C.R. 7017328449 - License: 5100000503
مطابق لكود البناء السعودي
ADCON Engineering Consultants

N

General Notes:

1. ALL DIMENSIONS ARE IN MM AND ANGLES IN DEGREES UNLESS OTHERWISE NOTED.
2. INTERIOR DESIGN DRAWINGS MUST ALWAYS BE READ IN CONJUNCTION WITH ALL OTHER RELEVANT SERVICES DRAWINGS AND CONTRACT DOCUMENTS.
3. ALL EXISTING OR PROPOSED ELEVATIONS (LEVELS) AND DIMENSIONS, ON SITE AND ON DRAWINGS MUST BE CHECKED AND VERIFIED BY THE CONTRACTOR BEFORE THE PREPARATION OF SHOP DRAWINGS OR COMMENCEMENT OF ANY ITEM OF WORK ON THE SITE.
4. ANY DISCREPANCY BETWEEN THESE DRAWINGS AND DOCUMENTS SHOULD BE REPORTED TO THE ENGINEER FOR CLARIFICATION AND VERIFICATION.

Keyplan:

	Description	Date	Rev.

Project Name:

MOSQUE

Address : **DAMMAM**
Saudi Arabia

Owner :

Plan : **GROUND FLOOR PLAN**

Scale : **1:10 MTS**

ADCON ENGINEERING CONSULTANTS
ادیکون للاستشارات الهندسية
LICENSE : 5100000503 C.R. : 2051230629
TEL : 054 - 4591667 P . O . BOX : 32272 / 3912


م . معماری ARCHITECT	م/ يوسف حراز	المشـــروع	جامع الاميرة سارة
م . كهربائى ELEC. ENGR.		المـــالك	وزارة الشؤن الاسلامية والاوقاف
م . ميكانيكا MECH. ENGR.		المـــوقع	الدمام
رسام اول DRAFTS MAN		رقم المخطط TOWN PLAN No.	١/٧٥
تدقيق المهندس ENGINEER CHECKER	م/ امل البقمى	رقم القطعة LOT No.	خ١/ب
		التـــاريخ DATE	

COMPUTATION OF AREAS جدول المساحات

مساحة الارض LOT AREA	٢٤٩١.٠٠ م٢ 2491.00sq.m	مساحة الملحق العلوى EXTENSION FLR AREA	م٢ sq.m
مساحة القبـــو BASEMENT FLOOR AREA	٠٠.٠٠ م٢ 00.00 sq.m	مساحة الميزانين MIZZANINE FLOOR	٠٠.٠٠ م٢ 00.00 sq.m
مساحة الدور الارضى GROUND FLOOR AREA	م٢ sq.m	طول الوارش PARAPET WALL	00.00 l.m.
مساحة الدور الاول FIRST FLOOR AREA	٠٠.٠٠ م٢ 00.00 sq.m	طول السور FENCE WALL	l.m.
مساحة الملحق الارضى ADD'L FLOOR AREA	٠٠.٠٠ م٢ 00.00 sq.m	نسبة البناء LOT COVERAGE %	%

Drawing Title:

Project Code:	Drawing No. :	Revision:
24-071	ID-GF-01	

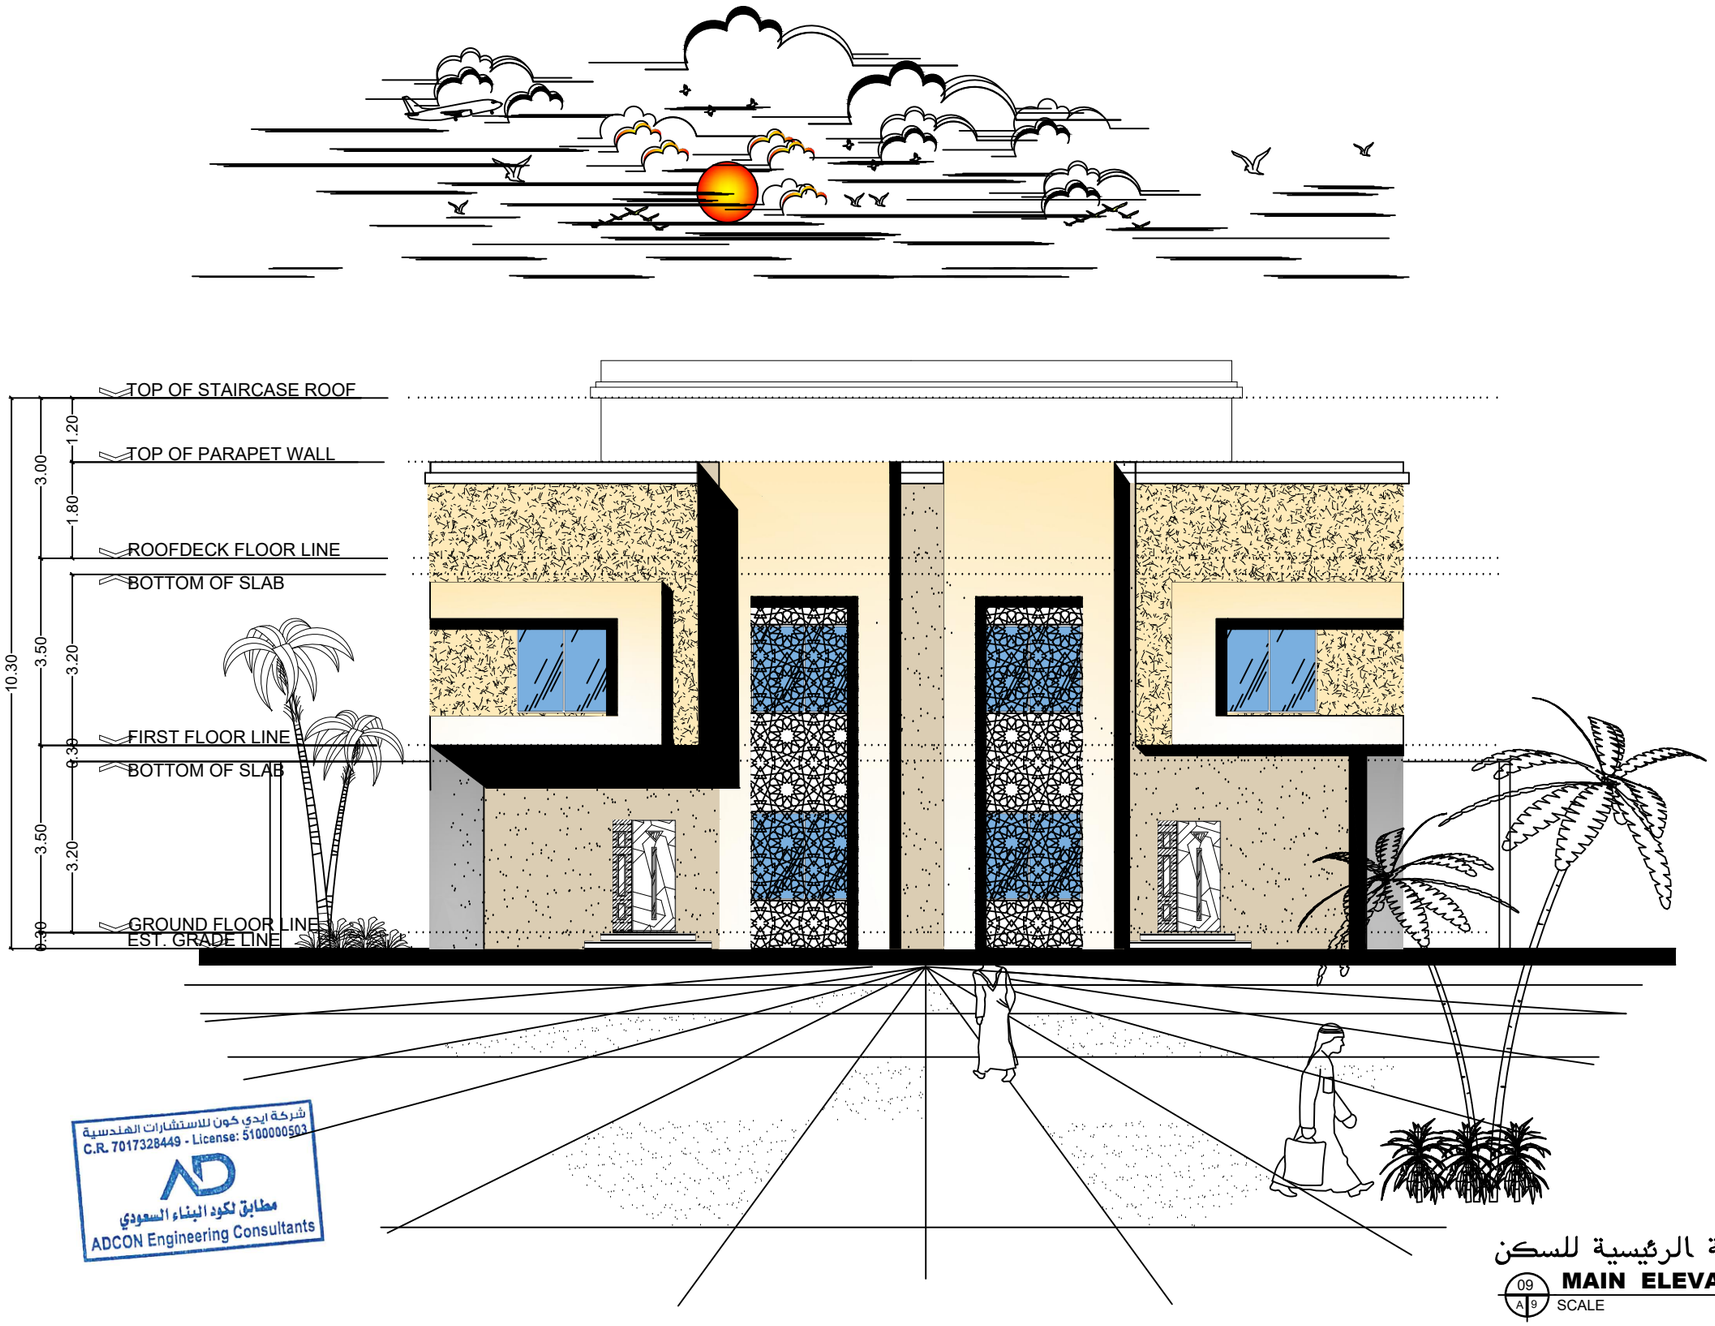

شركة ايدي كون للاستشارات الهندسية
C.R. 7017328449 - License: 5100000503
مطابق لكود البناء السعودي
ADCON Engineering Consultants

الواجهة الرئيسية للسكن

09 / A9 **MAIN ELEVATION**

SCALE 1:150M

N

General Notes:

1. ALL DIMENSIONS ARE IN MM AND ANGLES IN DEGREES UNLESS OTHERWISE NOTED.
2. INTERIOR DESIGN DRAWINGS MUST ALWAYS BE READ IN CONJUNCTION WITH ALL OTHER RELEVANT SERVICES DRAWINGS AND CONTRACT DOCUMENTS.
3. ALL EXISTING OR PROPOSED ELEVATIONS (LEVELS) AND DIMENSIONS, ON SITE AND ON DRAWINGS MUST BE CHECKED AND VERIFIED BY THE CONTRACTOR BEFORE THE PREPARATION OF SHOP DRAWINGS OR COMMENCEMENT OF ANY ITEM OF WORK ON THE SITE.
4. ANY DISCREPANCY BETWEEN THESE DRAWINGS AND DOCUMENTS SHOULD BE REPORTED TO THE ENGINEER FOR CLARIFICATION AND VERIFICATION.

Keyplan:

	Description	Date	Rev.

Project Name:

MOSQUE

Address : **DAMMAM**
Saudi Arabia

Owner :

Plan : **GROUND FLOOR PLAN**

Scale : **1:10 MTS**

ADCON ENGINEERING CONSULTANTS
اديكون للاستشارات الهندسية
LICENSE : 5100000503 C.R. : 2051230629
TEL : 054 - 4591667 P . O . BOX : 32272 / 3912


م . معماري ARCHITECT	م/ يوسف حراز	المشـــــروع	جامع الاميرة سارة
م . كهربائى ELEC. ENGR.		المـــــالك	وزارة الشؤن الاسلامية والاوقاف
م . ميكانيكا MECH. ENGR.		المـــــوقع	الدمام
رسام اول DRAFTS MAN		رقم المخطط TOWN PLAN No.	١/٧٥
تدقيق المهندس ENGINEER CHECKER	م/ امل البقمى	رقم القطعة LOT No.	خ١/ب
		التـــاريخ DATE	

جدول المساحات — COMPUTATION OF AREAS

مساحة الارض LOT AREA	٢٤٩١.٠٠ م٢ 2491.00 sq.m	مساحة الملحق العلوى EXTENSION FLR AREA	م٢ sq.m
مساحة القبـــو BASEMENT FLOOR AREA	٠.٠٠ م٢ 00.00 sq.m	مساحة الميزانين MIZZANINE FLOOR	٠.٠٠ م٢ 00.00 sq.m
مساحة الدور الارضى GROUND FLOOR AREA	م٢ sq.m	طول الوارش PARAPET WALL	00.00 l.m.
مساحة الدور الاول FIRST FLOOR AREA	٠.٠٠ م٢ 00.00 sq.m	طول السور FENCE WALL	l.m.
مساحة الملحق الارضى ADD'L FLOOR AREA	٠.٠٠ م٢ 00.00 sq.m	نسبة البناء LOT COVERAGE %	%


Drawing Title:

Project Code:	Drawing No. :	Revision:
24-071	ID-GF-01	

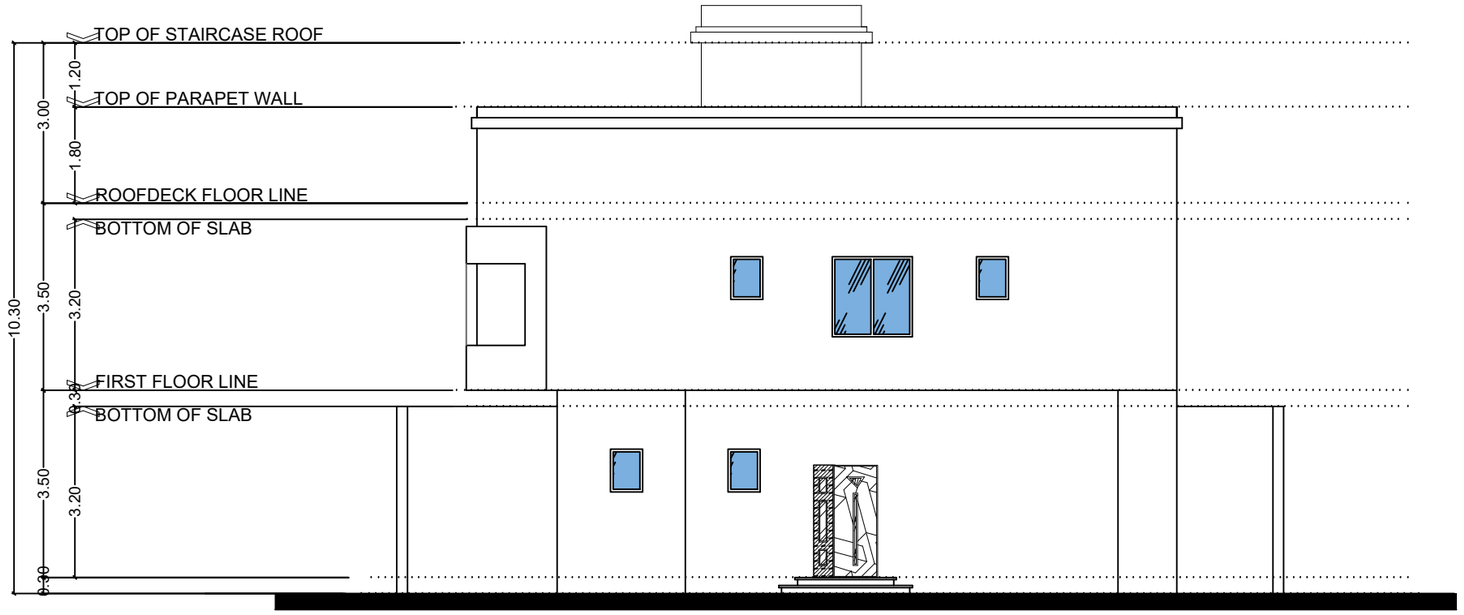

05 / A 5 **SIDE ELEVATION (EAST)**
SCALE 1:100M

شركة ايدي كون للاستشارات الهندسية
C.R. 7017328449 - License: 5100000503
مطابق لكود البناء السعودي
ADCON Engineering Consultants

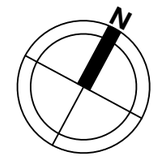

General Notes:

1. ALL DIMENSIONS ARE IN MM AND ANGLES IN DEGREES UNLESS OTHERWISE NOTED.
2. INTERIOR DESIGN DRAWINGS MUST ALWAYS BE READ IN CONJUNCTION WITH ALL OTHER RELEVANT SERVICES DRAWINGS AND CONTRACT DOCUMENTS.
3. ALL EXISTING OR PROPOSED ELEVATIONS (LEVELS) AND DIMENSIONS, ON SITE AND ON DRAWINGS MUST BE CHECKED AND VERIFIED BY THE CONTRACTOR BEFORE THE PREPARATION OF SHOP DRAWINGS OR COMMENCEMENT OF ANY ITEM OF WORK ON THE SITE.
4. ANY DISCREPANCY BETWEEN THESE DRAWINGS AND DOCUMENTS SHOULD BE REPORTED TO THE ENGINEER FOR CLARIFICATION AND VERIFICATION.

Keyplan:

	Description	Date	Rev.

Project Name:

MOSQUE

Address : **DAMMAM**
Saudi Arabia

Owner :

Plan : **GROUND FLOOR PLAN**
Scale : **1:10 MTS**

ADCON ENGINEERING CONSULTANTS
اديكون للاستشارات الهندسية
LICENSE : 5100000503 C.R. : 2051230629
TEL : 054 - 4591667 P . O . BOX : 32272 / 3912


م . معماري ARCHITECT	م/ يوسف حراز	المشـــــروع	جامع الاميرة سارة
م . كهربائي ELEC. ENGR.		المـــــالك	وزارة الشؤن الاسلامية والاوقاف
م . ميكانيكا MECH. ENGR.		المـــــوقع	الدمام
رسام اول DRAFTS MAN		رقم المخطط TOWN PLAN No.	١/٧٥
تدقيق المهندس ENGINEER CHECKER	م/ امل البقمى	رقم القطعة LOT No.	خ١/ب
		التـــاريخ DATE	

COMPUTATION OF AREAS جدول المساحات

مساحة الارض LOT AREA	٢٤٩١,٠٠ م٢ 2491.00sq.m	مساحة الملحق العلوى EXTENSION FLR AREA	م٢ sq.m
مساحة القبـــو BASEMENT FLOOR AREA	٠٠,٠٠ م٢ 00.00 sq.m	مساحة الميزانين MIZZANINE FLOOR	٠٠,٠٠ م٢ 00.00 sq.m
مساحة الدور الارضى GROUND FLOOR AREA	م٢ sq.m	طول الوارش PARAPET WALL	00.00 l.m.
مساحة الدور الاول FIRST FLOOR AREA	٠٠,٠٠ م٢ 00.00 sq.m	طول السور FENCE WALL	l.m.
مساحة الملحق الارضى ADD'L FLOOR AREA	٠٠,٠٠ م٢ 00.00 sq.m	نسبة البناء % LOT COVERAGE	%

Drawing Title:

Project Code:	Drawing No. :	Revision:
24-071	**ID-GF-01**	

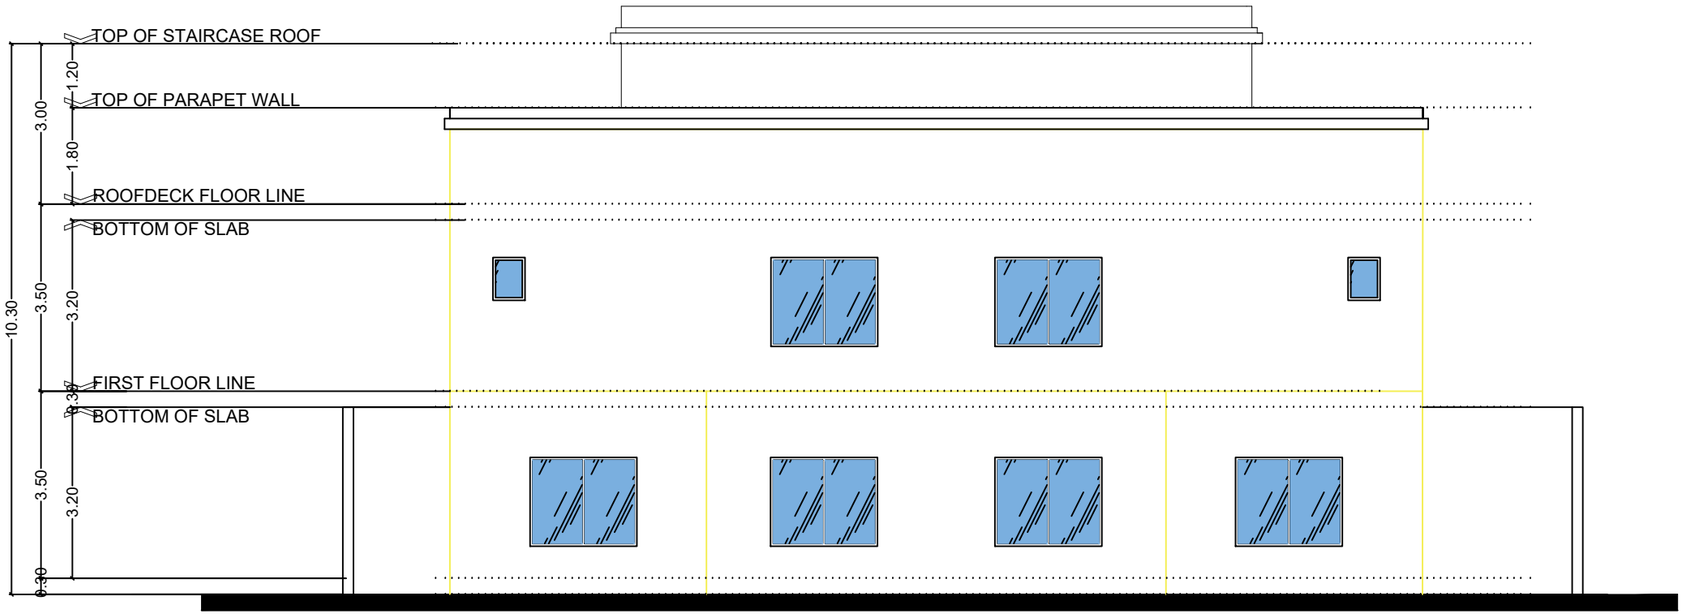

04 / A4 **SIDE ELEVATION (SOUTH)**

SCALE 1:100M

N

General Notes:

1. ALL DIMENSIONS ARE IN MM AND ANGLES IN DEGREES UNLESS OTHERWISE NOTED.
2. INTERIOR DESIGN DRAWINGS MUST ALWAYS BE READ IN CONJUNCTION WITH ALL OTHER RELEVANT SERVICES DRAWINGS AND CONTRACT DOCUMENTS.
3. ALL EXISTING OR PROPOSED ELEVATIONS (LEVELS) AND DIMENSIONS, ON SITE AND ON DRAWINGS MUST BE CHECKED AND VERIFIED BY THE CONTRACTOR BEFORE THE PREPARATION OF SHOP DRAWINGS OR COMMENCEMENT OF ANY ITEM OF WORK ON THE SITE.
4. ANY DISCREPANCY BETWEEN THESE DRAWINGS AND DOCUMENTS SHOULD BE REPORTED TO THE ENGINEER FOR CLARIFICATION AND VERIFICATION.

Keyplan:

	Description	Date	Rev.

Project Name:

MOSQUE

Address : **DAMMAM**
Saudi Arabia

Owner :

Plan : **GROUND FLOOR PLAN**

Scale : **1:10 MTS**

ADCON ENGINEERING CONSULTANTS
اديكون للاستشارات الهندسية
LICENSE : 5100000503 C.R. : 2051230629
TEL : 054 - 4591667 P . O . BOX : 32272 / 3912


م . معماري ARCHITECT	م/ يوسف حراز	المشـــــروع	جامع الاميرة سارة
م . كهربائي ELEC. ENGR.		المـــــالك	وزارة الشؤن الاسلامية والاوقاف
م . ميكانيكا MECH. ENGR.		المـــــوقع	الدمام
رسام اول DRAFTS MAN		رقم المخطط TOWN PLAN No.	١/٧٥
تدقيق المهندس ENGINEER CHECKER	م/ امل البقمى	رقم القطعة LOT No.	خ/ب
		التـــاريخ DATE	

جدول المساحات — COMPUTATION OF AREAS


مساحة الارض LOT AREA	٢٤٩١.٠٠ م٢ 2491.00sq.m	مساحة الملحق العلوى EXTENSION FLR AREA	م٢ sq.m
مساحة القبـــو BASEMENT FLOOR AREA	٠.٠٠ م٢ 00.00 sq.m	مساحة الميزانين MIZZANINE FLOOR	٠.٠٠ م٢ 00.00 sq.m
مساحة الدور الارضى GROUND FLOOR AREA	م٢ sq.m	طول الوارش PARAPET WALL	00.00 l.m.
مساحة الدور الاول FIRST FLOOR AREA	٠.٠٠ م٢ 00.00 sq.m	طول السور FENCE WALL	l.m.
مساحة الملحق الارضى ADD'L FLOOR AREA	٠.٠٠ م٢ 00.00 sq.m	نسبة البناء % LOT COVERAGE	%

Drawing Title:

Project Code:	Drawing No. :	Revision:
24-071	ID-GF-01	

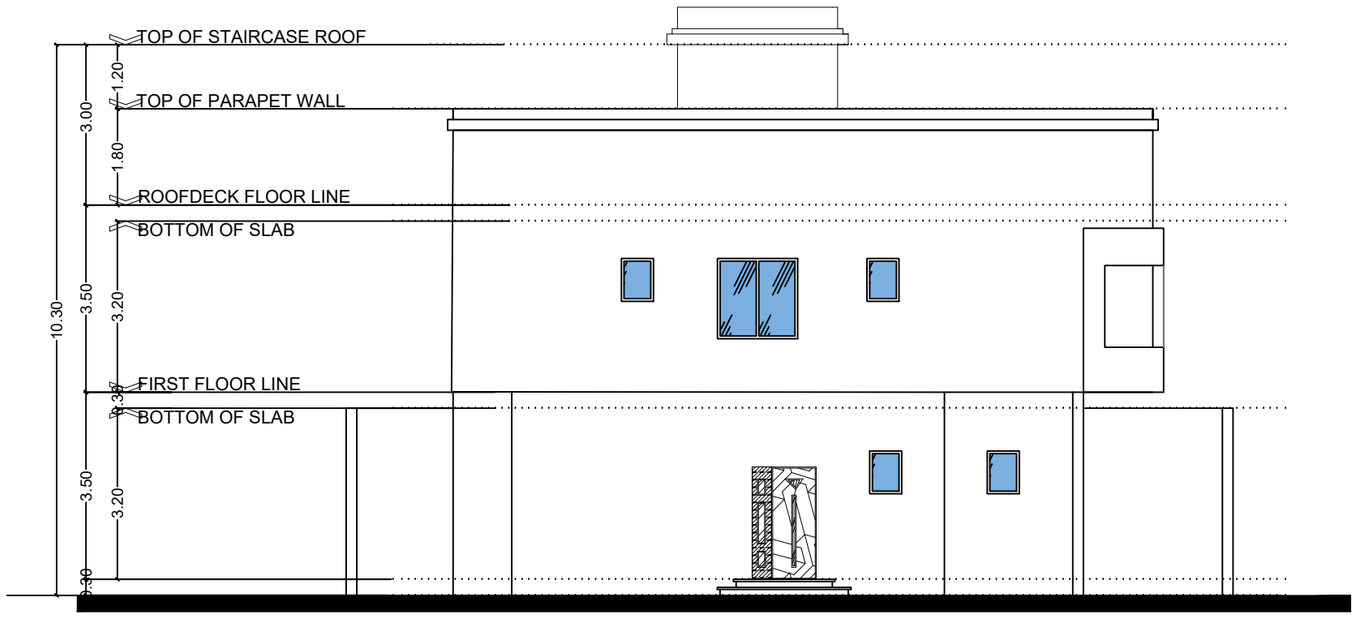

05 / A 5 **SIDE ELEVATION (NORTH)**
SCALE 1:100M

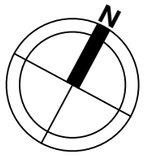

General Notes:

1. ALL DIMENSIONS ARE IN MM AND ANGLES IN DEGREES UNLESS OTHERWISE NOTED.
2. INTERIOR DESIGN DRAWINGS MUST ALWAYS BE READ IN CONJUNCTION WITH ALL OTHER RELEVANT SERVICES DRAWINGS AND CONTRACT DOCUMENTS.
3. ALL EXISTING OR PROPOSED ELEVATIONS (LEVELS) AND DIMENSIONS, ON SITE AND ON DRAWINGS MUST BE CHECKED AND VERIFIED BY THE CONTRACTOR BEFORE THE PREPARATION OF SHOP DRAWINGS OR COMMENCEMENT OF ANY ITEM OF WORK ON THE SITE.
4. ANY DISCREPANCY BETWEEN THESE DRAWINGS AND DOCUMENTS SHOULD BE REPORTED TO THE ENGINEER FOR CLARIFICATION AND VERIFICATION.

Keyplan:

	Description	Date	Rev.

Project Name:

MOSQUE

Address : **DAMMAM**
Saudi Arabia

Owner :

Plan : **GROUND FLOOR PLAN**

Scale : **1:10 MTS**

ADCON ENGINEERING CONSULTANTS
اديكون للاستشارات الهندسية
LICENSE : 5100000503 C.R. : 2051230629
TEL : 054 - 4591667 P . O . BOX : 32272 / 3912

م . معماري ARCHITECT	م/ يوسف حراز	المشـــــروع	جامع الاميرة سارة
م . كهربائي ELEC. ENGR.		المـــــــالك	وزارة الشؤن الاسلامية والاوقاف
م . ميكانيكا MECH. ENGR.		المـــــوقع	الدمام
رسام اول DRAFTS MAN		رقم المخطط TOWN PLAN No.	١/٧٥
تدقيق المهندس ENGINEER CHECKER	م/ امل البقمى	رقم القطعة LOT No.	خ١/ب
		التـــاريخ DATE	

COMPUTATION OF AREAS — جدول المساحات

مساحة الارض LOT AREA	٢٤٩١.٠٠ م٢ 2491.00 sq.m	مساحة الملحق العلوى EXTENSION FLR AREA	م٢ sq.m
مساحة القبـــو BASEMENT FLOOR AREA	٠.٠٠ م٢ 00.00 sq.m	مساحة الميزانين MIZZANINE FLOOR	٠.٠٠ م٢ 00.00 sq.m
مساحة الدور الارضى GROUND FLOOR AREA	م٢ sq.m	طول الوارش PARAPET WALL	00.00 l.m.
مساحة الدور الاول FIRST FLOOR AREA	٠.٠٠ م٢ 00.00 sq.m	طول السور FENCE WALL	l.m.
مساحة الملحق الارضى ADD'L FLOOR AREA	٠.٠٠ م٢ 00.00 sq.m	نسبة البناء LOT COVERAGE %	%

Drawing Title:

Project Code:	Drawing No. :	Revision:
24-071	ID-GF-01	